39/78

PLAT BOOK PAGE NO

MEADOW POINTE PARCEL 17 UNIT 3

SECTION 33, TOWNSHIP 26 SOUTH, RANGE 20 EAST, PASCO COUNTY, FLORIDA

CABLE TELEVISION NOTE

Utility easements shall provide that such easements shall also be easements for the construction, installation, maintenance, and operation of cable television services, provided, however, no such construction, installation, maintenance, and operation of cable television services shall interfere with the facilities and services of an electric, telephone, gas or other public utility


State Plane Coordinates as shown hereon are in compliance with National Ocean Service standards with geodetic positions rigidly adjusted to the North America Datum of 1983 as readjusted in 1990


N

SCALE 1" = 200'

0 100 200 400

SCALE IN FEET

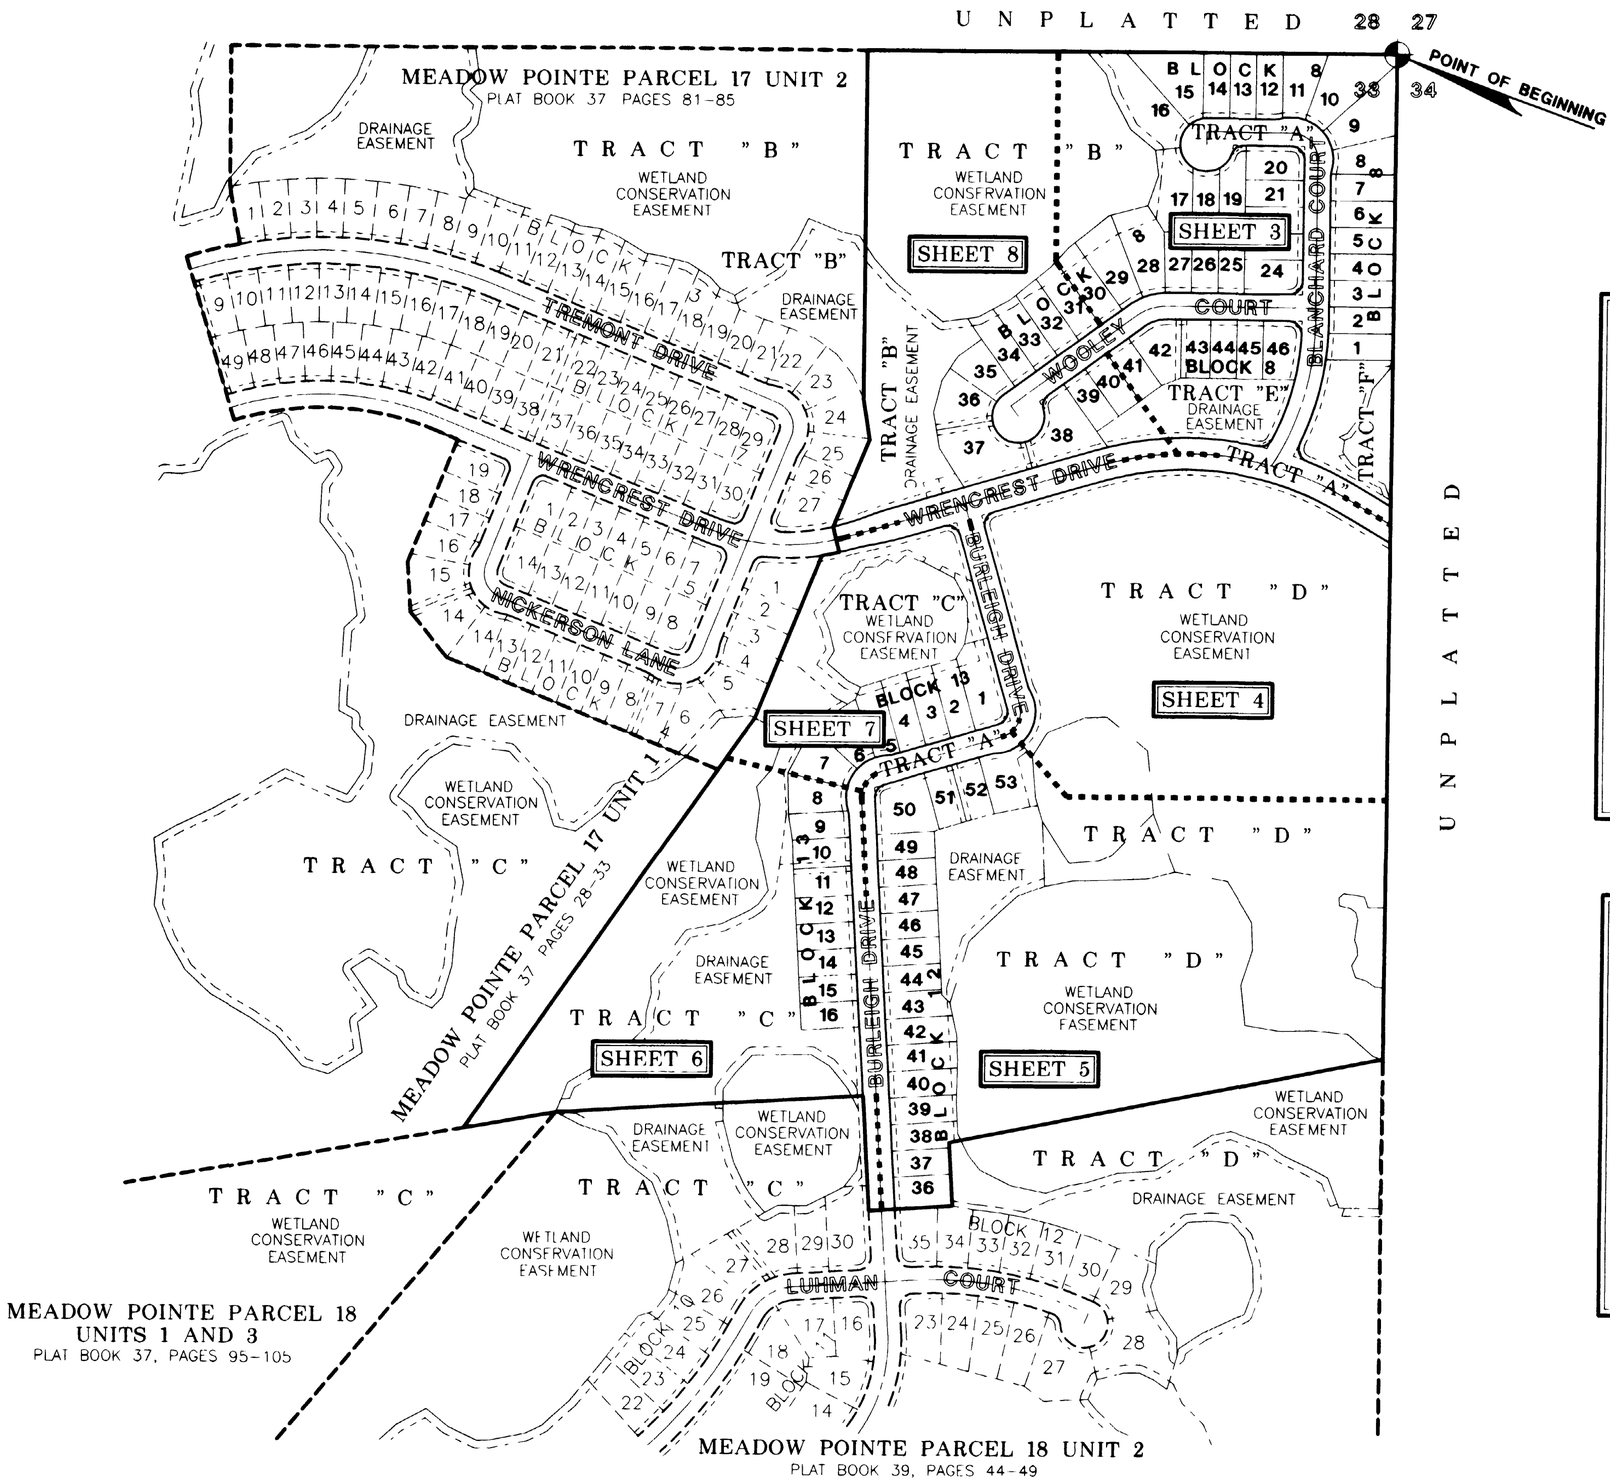

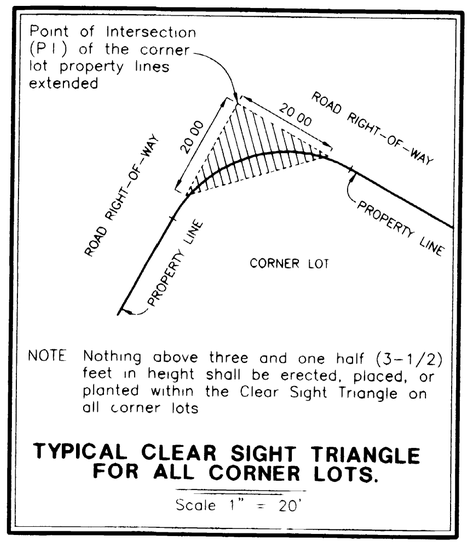


NOTE Nothing above three and one half (3-1/2) feet in height shall be erected, placed, or planted within the Clear Sight Triangle on all corner lots

TYPICAL CLEAR SIGHT TRIANGLE FOR ALL CORNER LOTS.

Scale 1" = 20'

Note In the case where the location of a P C P falls in the top of a Sanitary Manhole or other Utility Structure and it can not be set, four (4) reference points are set establishing two lines that intersect at the P C P location

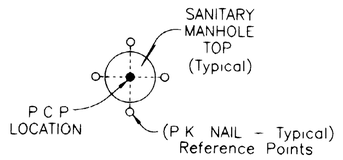

P.C.P. REFERENCE DIAGRAM

(NOT TO SCALE)

KEY SHEET

NOTE REFER TO THE FOLLOWING SHEETS OF THIS PLAT FOR DETAILED LABELLING AND DIMENSIONING

2212 SWANN AVENUE
TAMPA, FLORIDA 33606
(813) 253-5311

HEIDT & ASSOCIATES, INC
LICENSED BUSINESS NUMBER LB148
CIVIL ENGINEERING
LAND SURVEYING