
39/79

PLAT BOOK PAGE NO


MEADOW POINTE PARCEL 17 UNIT 3

SECTION 33, TOWNSHIP 26 SOUTH, RANGE 20 EAST, PASCO COUNTY, FLORIDA

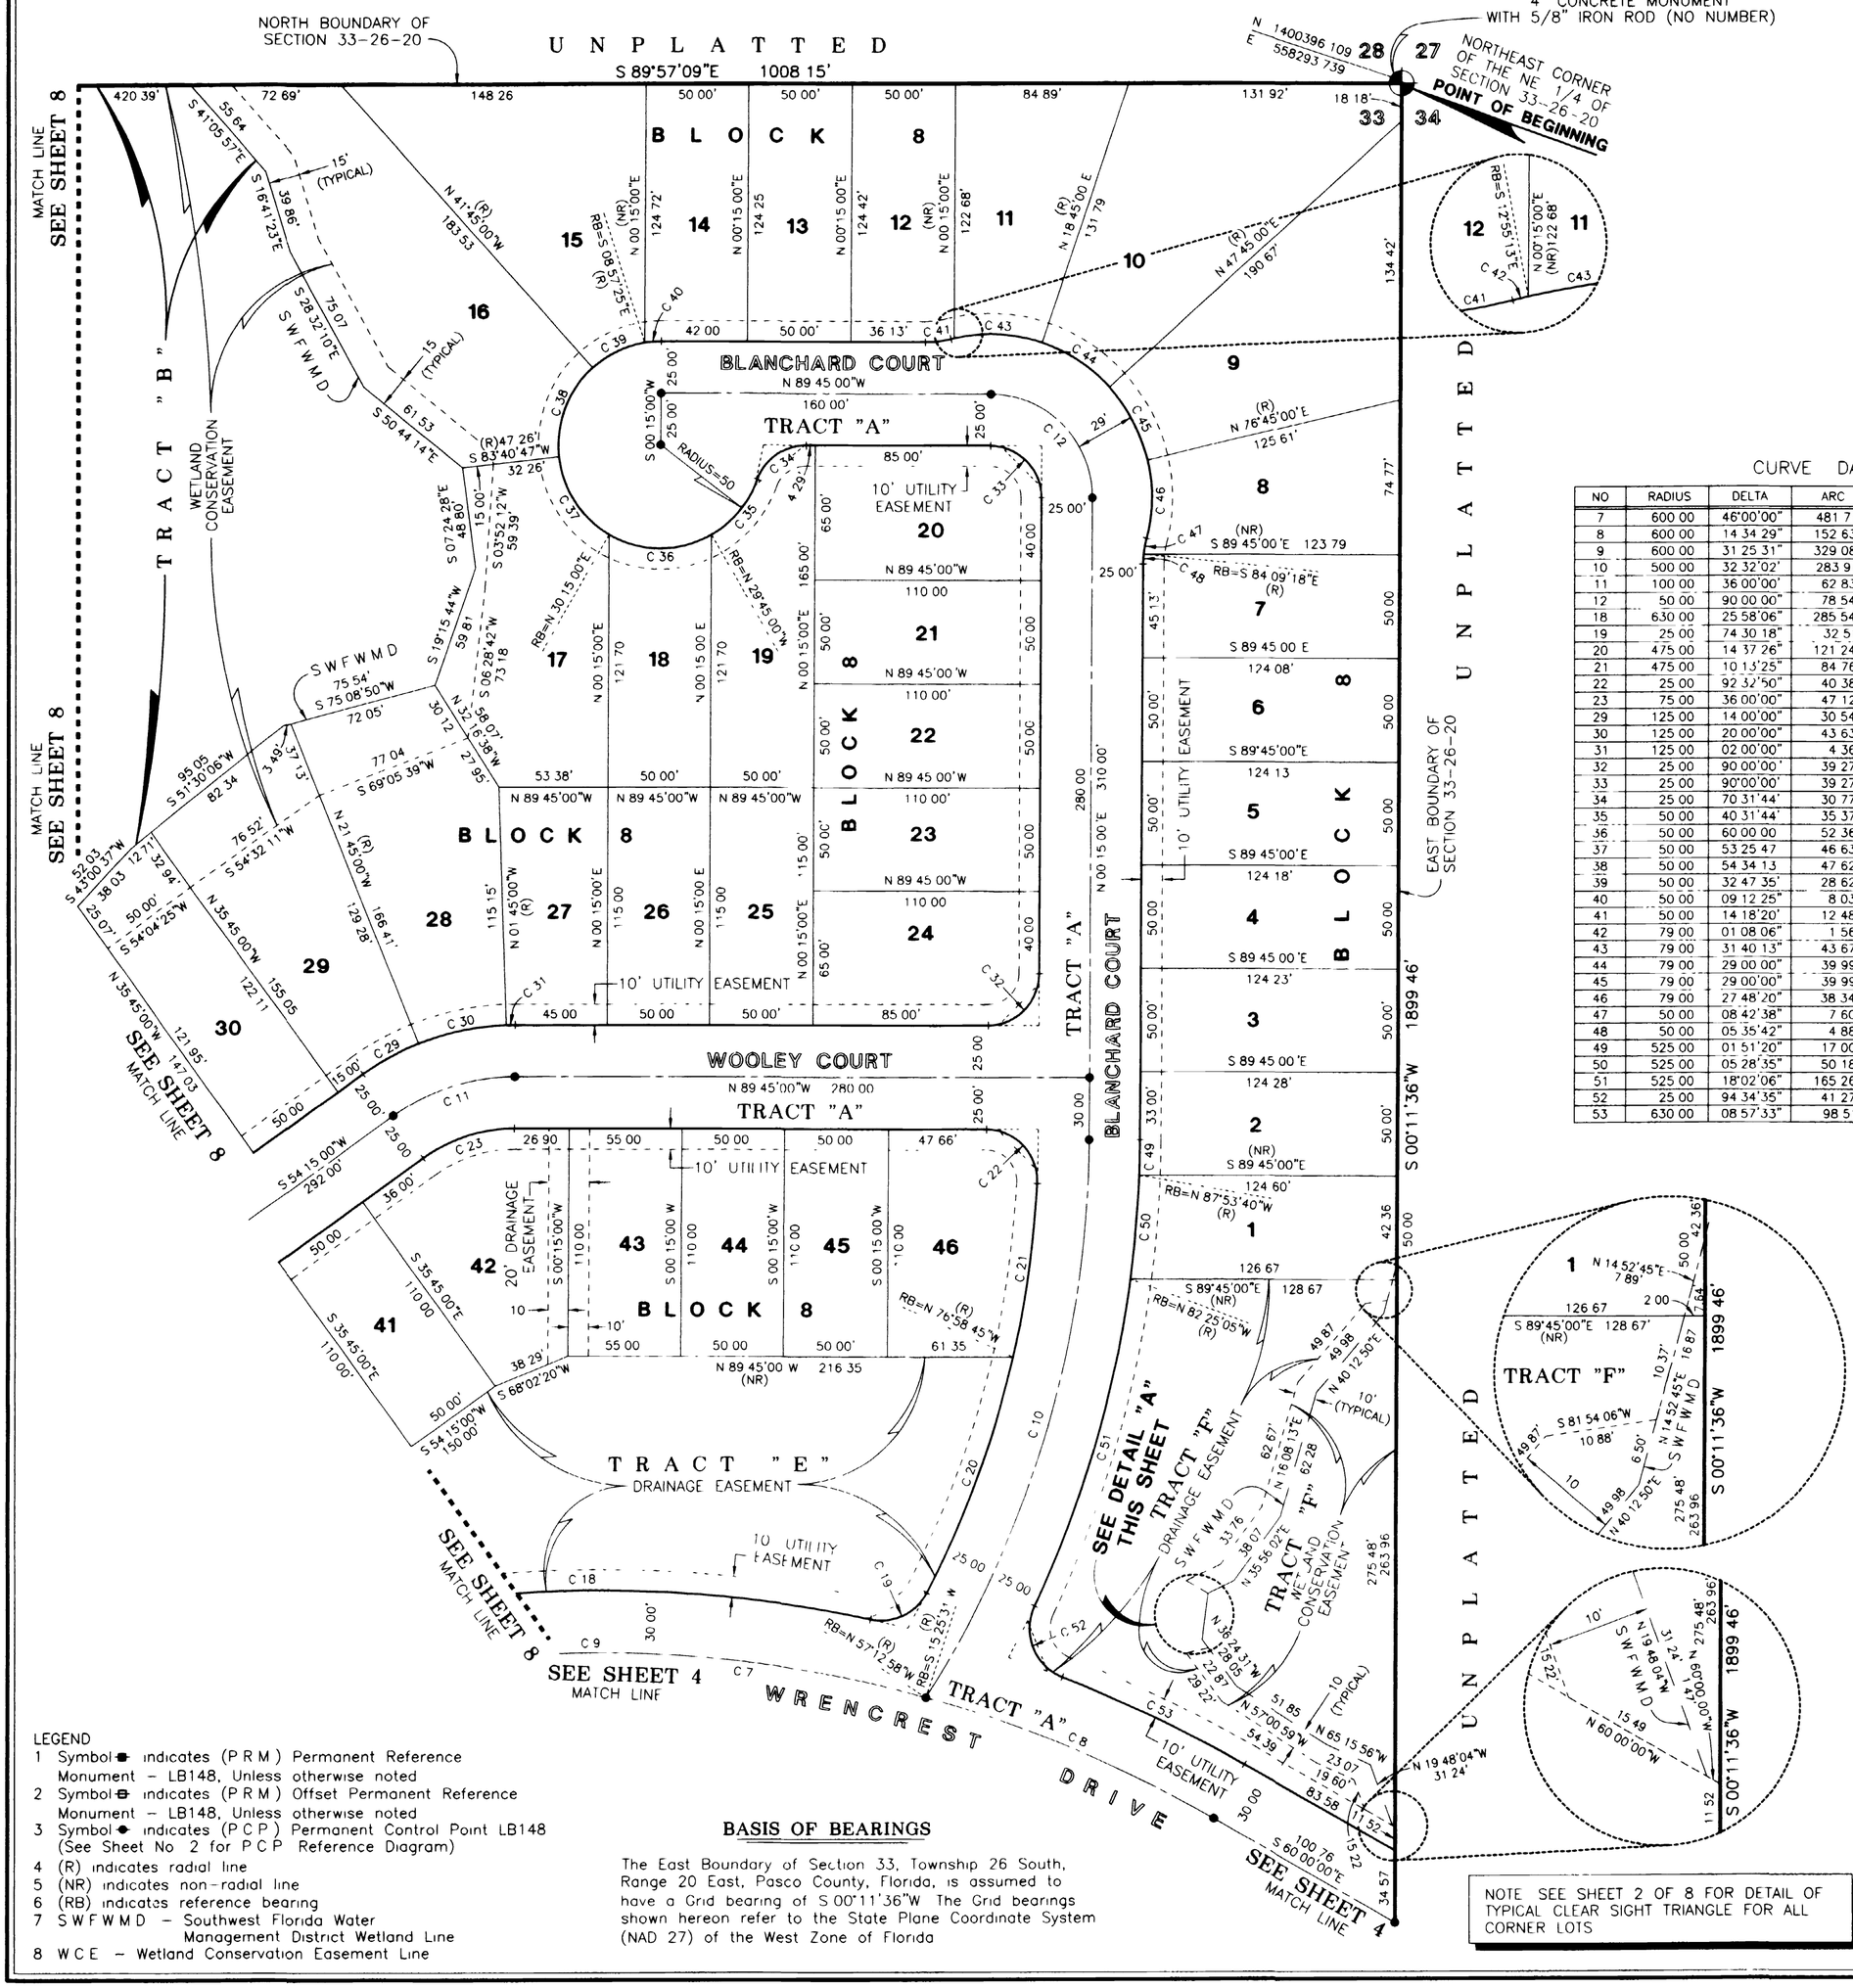

CURVE DATA TABLE

NO	RADIUS	DELTA	ARC	TANGENT	CHORD	BEARING
7	600 00	46°00'00"	481 71	254 68	468 88	S 83°00 00"E
8	600 00	14 34 29"	152 63	76 73	152 22	N 67 17 15"W
9	600 00	31 25 31"	329 08	168 79	324 97	S 89 42'45"W
10	500 00	32 32'02"	283 91	145 90	280 11	N 16 31 01"E
11	100 00	36 00'00"	62 83	32 49	61 80	S 72 15'00"W
12	50 00	90 00 00"	78 54	50 00	70 71	N 44 45 00"W
18	630 00	25 58'06"	285 54	145 26	283 10	N 89 09'56"E
19	25 00	74 30 18"	32 51	19 01	30 27	N 64 53'50"E
20	475 00	14 37 26"	121 24	60 95	120 91	N 20 19'58"E
21	475 00	10 13'25"	84 76	42 49	84 64	N 07 54 33"E
22	25 00	92 32'50"	40 38	26 14	36 13	N 43 28'35"W
23	75 00	36 00'00"	47 12	24 37	46 35	S 72 15 00"W
29	125 00	14 00'00"	30 54	15 35	30 47	N 61°15 00"E
30	125 00	20 00'00"	43 63	22 04	43 41	N 78 15 00"E
31	125 00	02 00'00"	4 36	2 18	4 36	N 89 15 00"E
32	25 00	90 00'00"	39 27	25 00	35 36	N 45 15 00"E
33	25 00	90°00'00"	39 27	25 00	35 36	N 44°45 00"W
34	25 00	70 31'44"	30 77	17 68	28 87	S 54 59'08"W
35	50 00	40 31'44"	35 37	18 46	34 64	S 39°59'08"W
36	50 00	60 00 00	52 36	28 87	50 00	N 89 45'00"W
37	50 00	53 25 47	46 63	25 16	44 96	N 33 02'07"W
38	50 00	54 34 13	47 62	25 79	45 84	N 20 57'53"E
39	50 00	32 47 35'	28 62	14 71	28 23	N 64 38'48"E
40	50 00	09 12 25"	8 03	4 03	8 03	N 85 38'48"E
41	50 00	14 18'20'	12 48	6 27	12 45	N 83 05'50"E
42	79 00	01 08 06"	1 56	0 78	1 56	N 76 30'43"E
43	79 00	31 40 13"	43 67	22 41	43 11	S 87 05'07"E
44	79 00	29 00 00"	39 99	20 43	39 56	S 56 45'00"E
45	79 00	29 00'00"	39 99	20 43	39 56	S 27 45'00"E
46	79 00	27 48'20"	38 34	19 55	37 96	S 00 39'10"W
47	50 00	08 42'38"	7 60	3 81	7 59	S 10°12'01"W
48	50 00	05 35'42"	4 88	2 44	4 88	S 03 02'51"W
49	525 00	01 51'20"	17 00	8 50	17 00	S 01 10'40"W
50	525 00	05 28'35"	50 18	25 11	50 16	S 04 50 38"W
51	525 00	18°02'06"	165 26	83 32	164 57	S 16 35 59"W
52	25 00	94 34'35"	41 27	27 08	36 74	S 21 40 16"E
53	630 00	08 57'33"	98 51	49 36	98 41	S 64 28 47"E

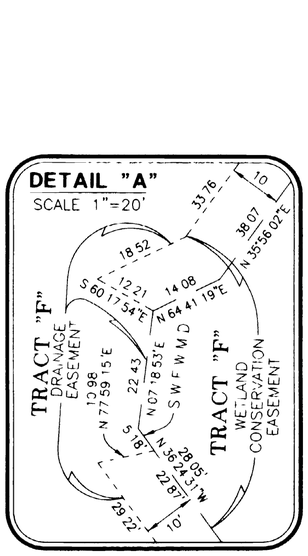

LEGEND

1 Symbol ■ indicates (P R M) Permanent Reference Monument – LB148, Unless otherwise noted
2 Symbol ⊕ indicates (P R M) Offset Permanent Reference Monument – LB148, Unless otherwise noted
3 Symbol ● indicates (P C P) Permanent Control Point LB148 (See Sheet No 2 for P C P Reference Diagram)
4 (R) indicates radial line
5 (NR) indicates non-radial line
6 (RB) indicates reference bearing
7 S W F W M D – Southwest Florida Water Management District Wetland Line
8 W C E – Wetland Conservation Easement Line

BASIS OF BEARINGS

The East Boundary of Section 33, Township 26 South, Range 20 East, Pasco County, Florida, is assumed to have a Grid bearing of S 00°11'36"W The Grid bearings shown hereon refer to the State Plane Coordinate System (NAD 27) of the West Zone of Florida

NOTE SEE SHEET 2 OF 8 FOR DETAIL OF TYPICAL CLEAR SIGHT TRIANGLE FOR ALL CORNER LOTS

2212 SWANN AVENUE
TAMPA FLORIDA 33606
(813) 253-5311

HEIDT & ASSOCIATES, INC
LICENSED BUSINESS NUMBER LB148
CIVIL ENGINEERING
LAND SURVEYING