
39/80

PLAT BOOK PAGE NO

MEADOW POINTE PARCEL 17 UNIT 3

SECTION 33, TOWNSHIP 26 SOUTH, RANGE 20 EAST, PASCO COUNTY, FLORIDA

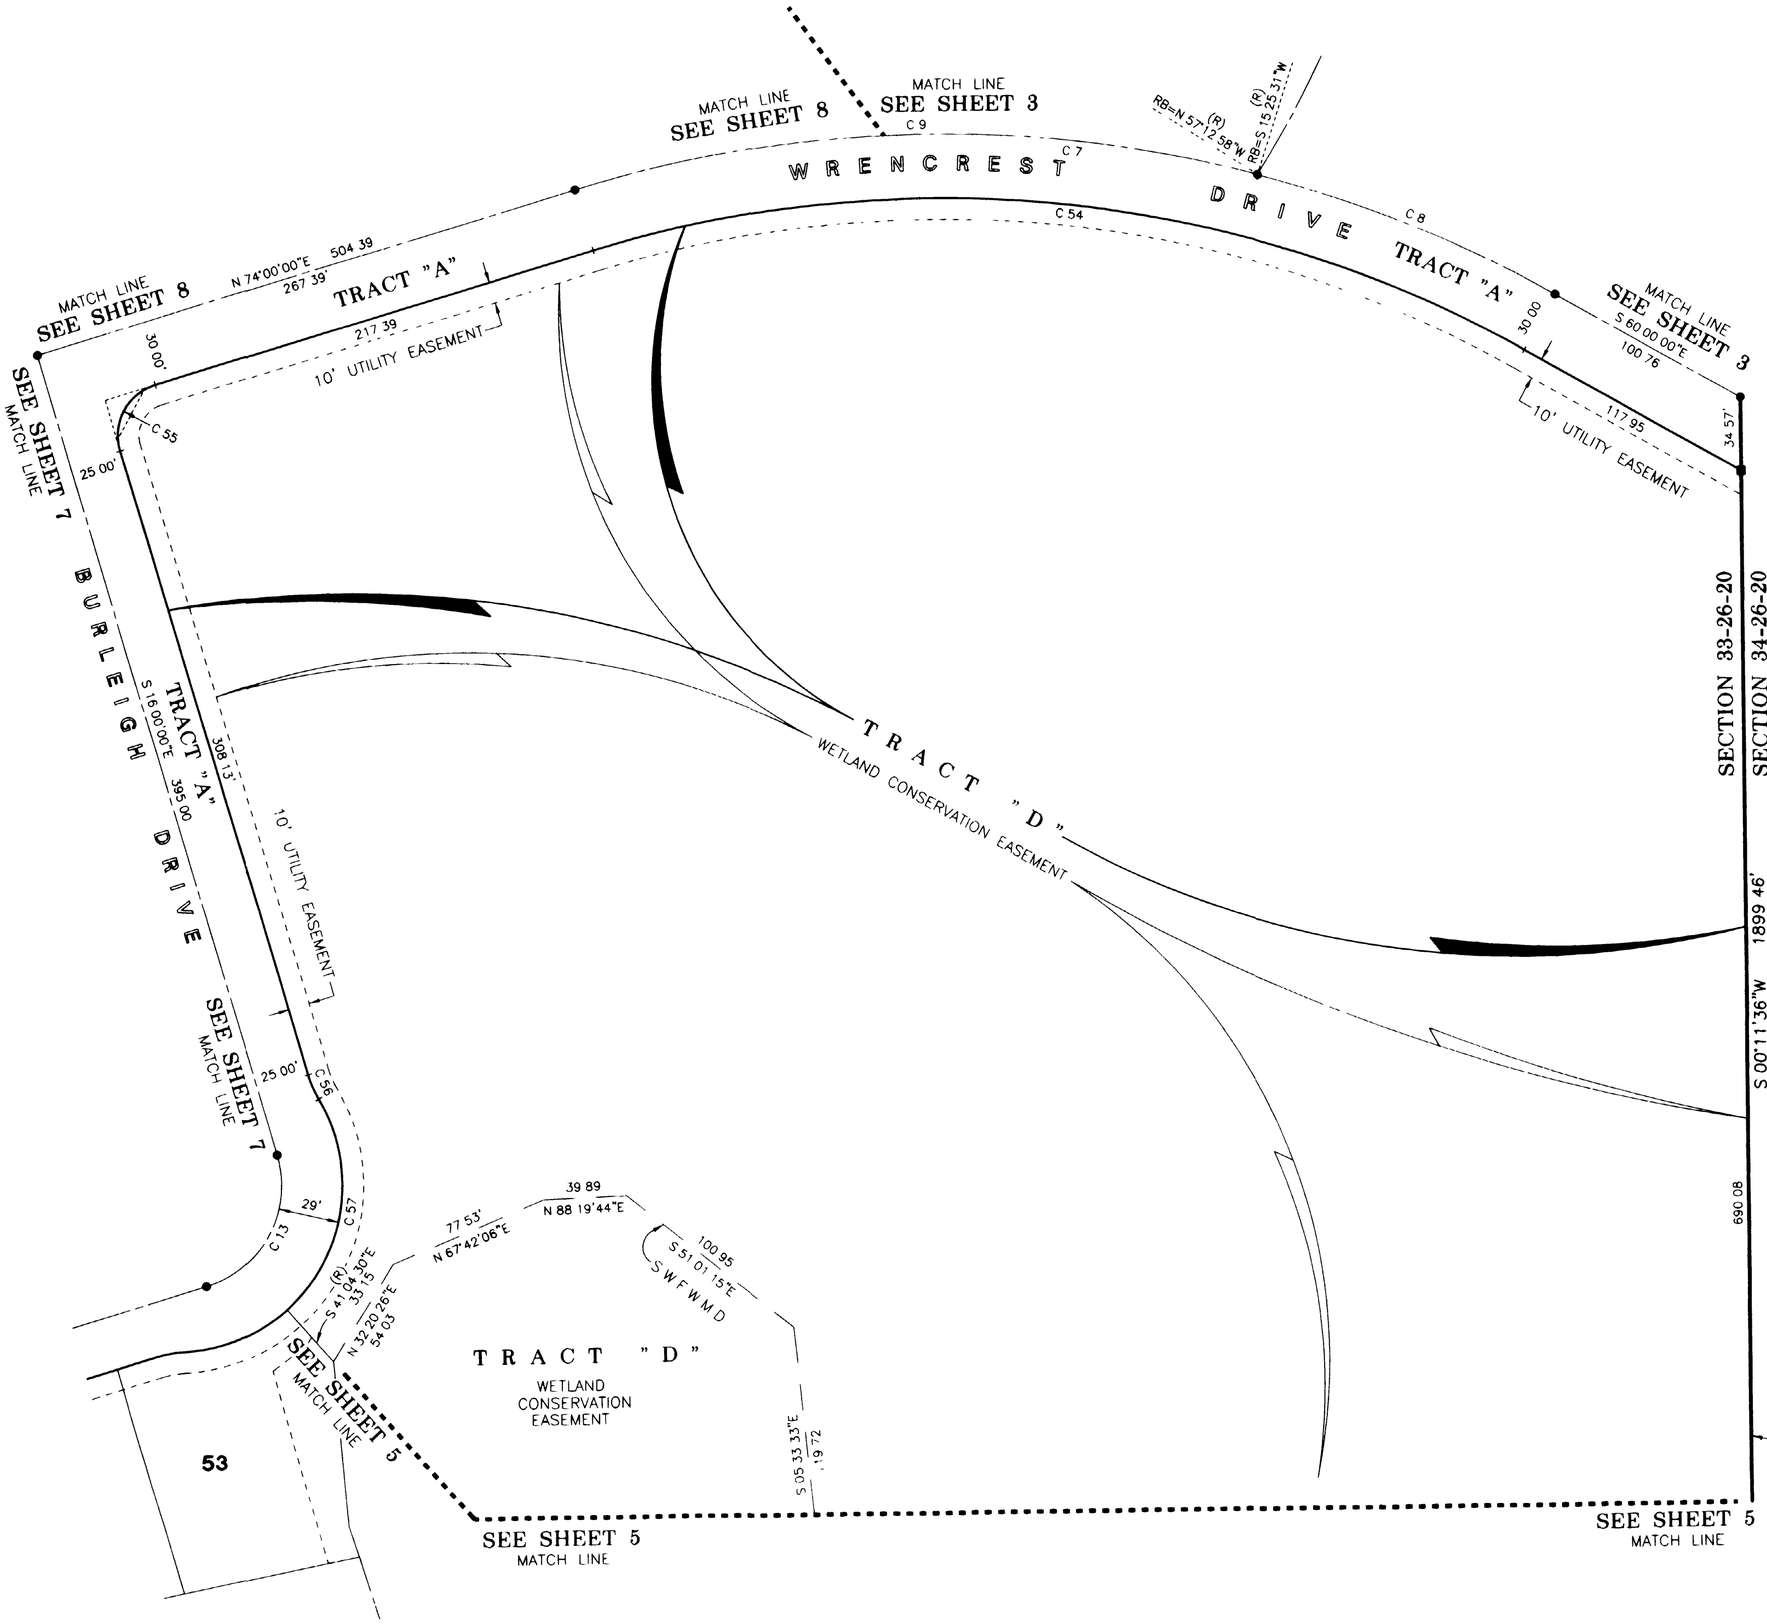

N

SCALE 1" = 50'

0 25 50 100

SCALE IN FEET

SEE NOTE ON SHEET 3 OF 8 FOR BASIS OF BEARINGS

LEGEND

1 Symbol ■ indicates (P R M) Permanent Reference Monument – LB148, Unless otherwise noted
2 Symbol ⊟ indicates (P R M) Offset Permanent Reference Monument – LB148, Unless otherwise noted
3 Symbol ◆ indicates (P C P) Permanent Control Point LB148 (See Sheet No 2 for P C P Reference Diagram)
4 (R) indicates radial line
5 (NR) indicates non-radial line
6 (RB) indicates reference bearing
7 S W F W M D – Southwest Florida Water Management District Wetland Line
8 W C E – Wetland Conservation Easement Line

CURVE DATA TABLE

NO	RADIUS	DELTA	ARC	TANGENT	CHORD	BEARING
7	600 00	46°00'00"	481 71	254 68	468 88	S 83°00'00"E
8	600 00	14 34'29"	152 63	76 73	152 22	N 67 17'15"W
9	600 00	31 25 31'	329 08	168 79	324 97	S 89 42 45"W
13	50 00	90°00'00"	78 54	50 00	70 71	S 29°00'00"W
54	570 00	46 00'00"	457 63	241 95	445 43	N 83 00'00"W
55	25 00	90 00'00"	39 27	25 00	35 36	S 29°00 00"W
56	50 00	14 18 20"	12 48	6 27	12 45	S 23°09 10"E
57	79 00	79°13'50"	109 24	65 39	100 75	S 09°18'35"W

NOTE SEE SHEET 2 OF 8 FOR DETAIL OF TYPICAL CLEAR SIGHT TRIANGLE FOR ALL CORNER LOTS

2212 SWANN AVENUE
TAMPA, FLORIDA 33606
(813) 253-5311
HEIDT & ASSOCIATES, INC
LICENSED BUSINESS NUMBER LB148
CIVIL ENGINEERING
LAND SURVEYING