
39/83

PLAT BOOK PAGE NO

MEADOW POINTE PARCEL 17 UNIT 3

SECTION 33, TOWNSHIP 26 SOUTH, RANGE 20 EAST, PASCO COUNTY, FLORIDA

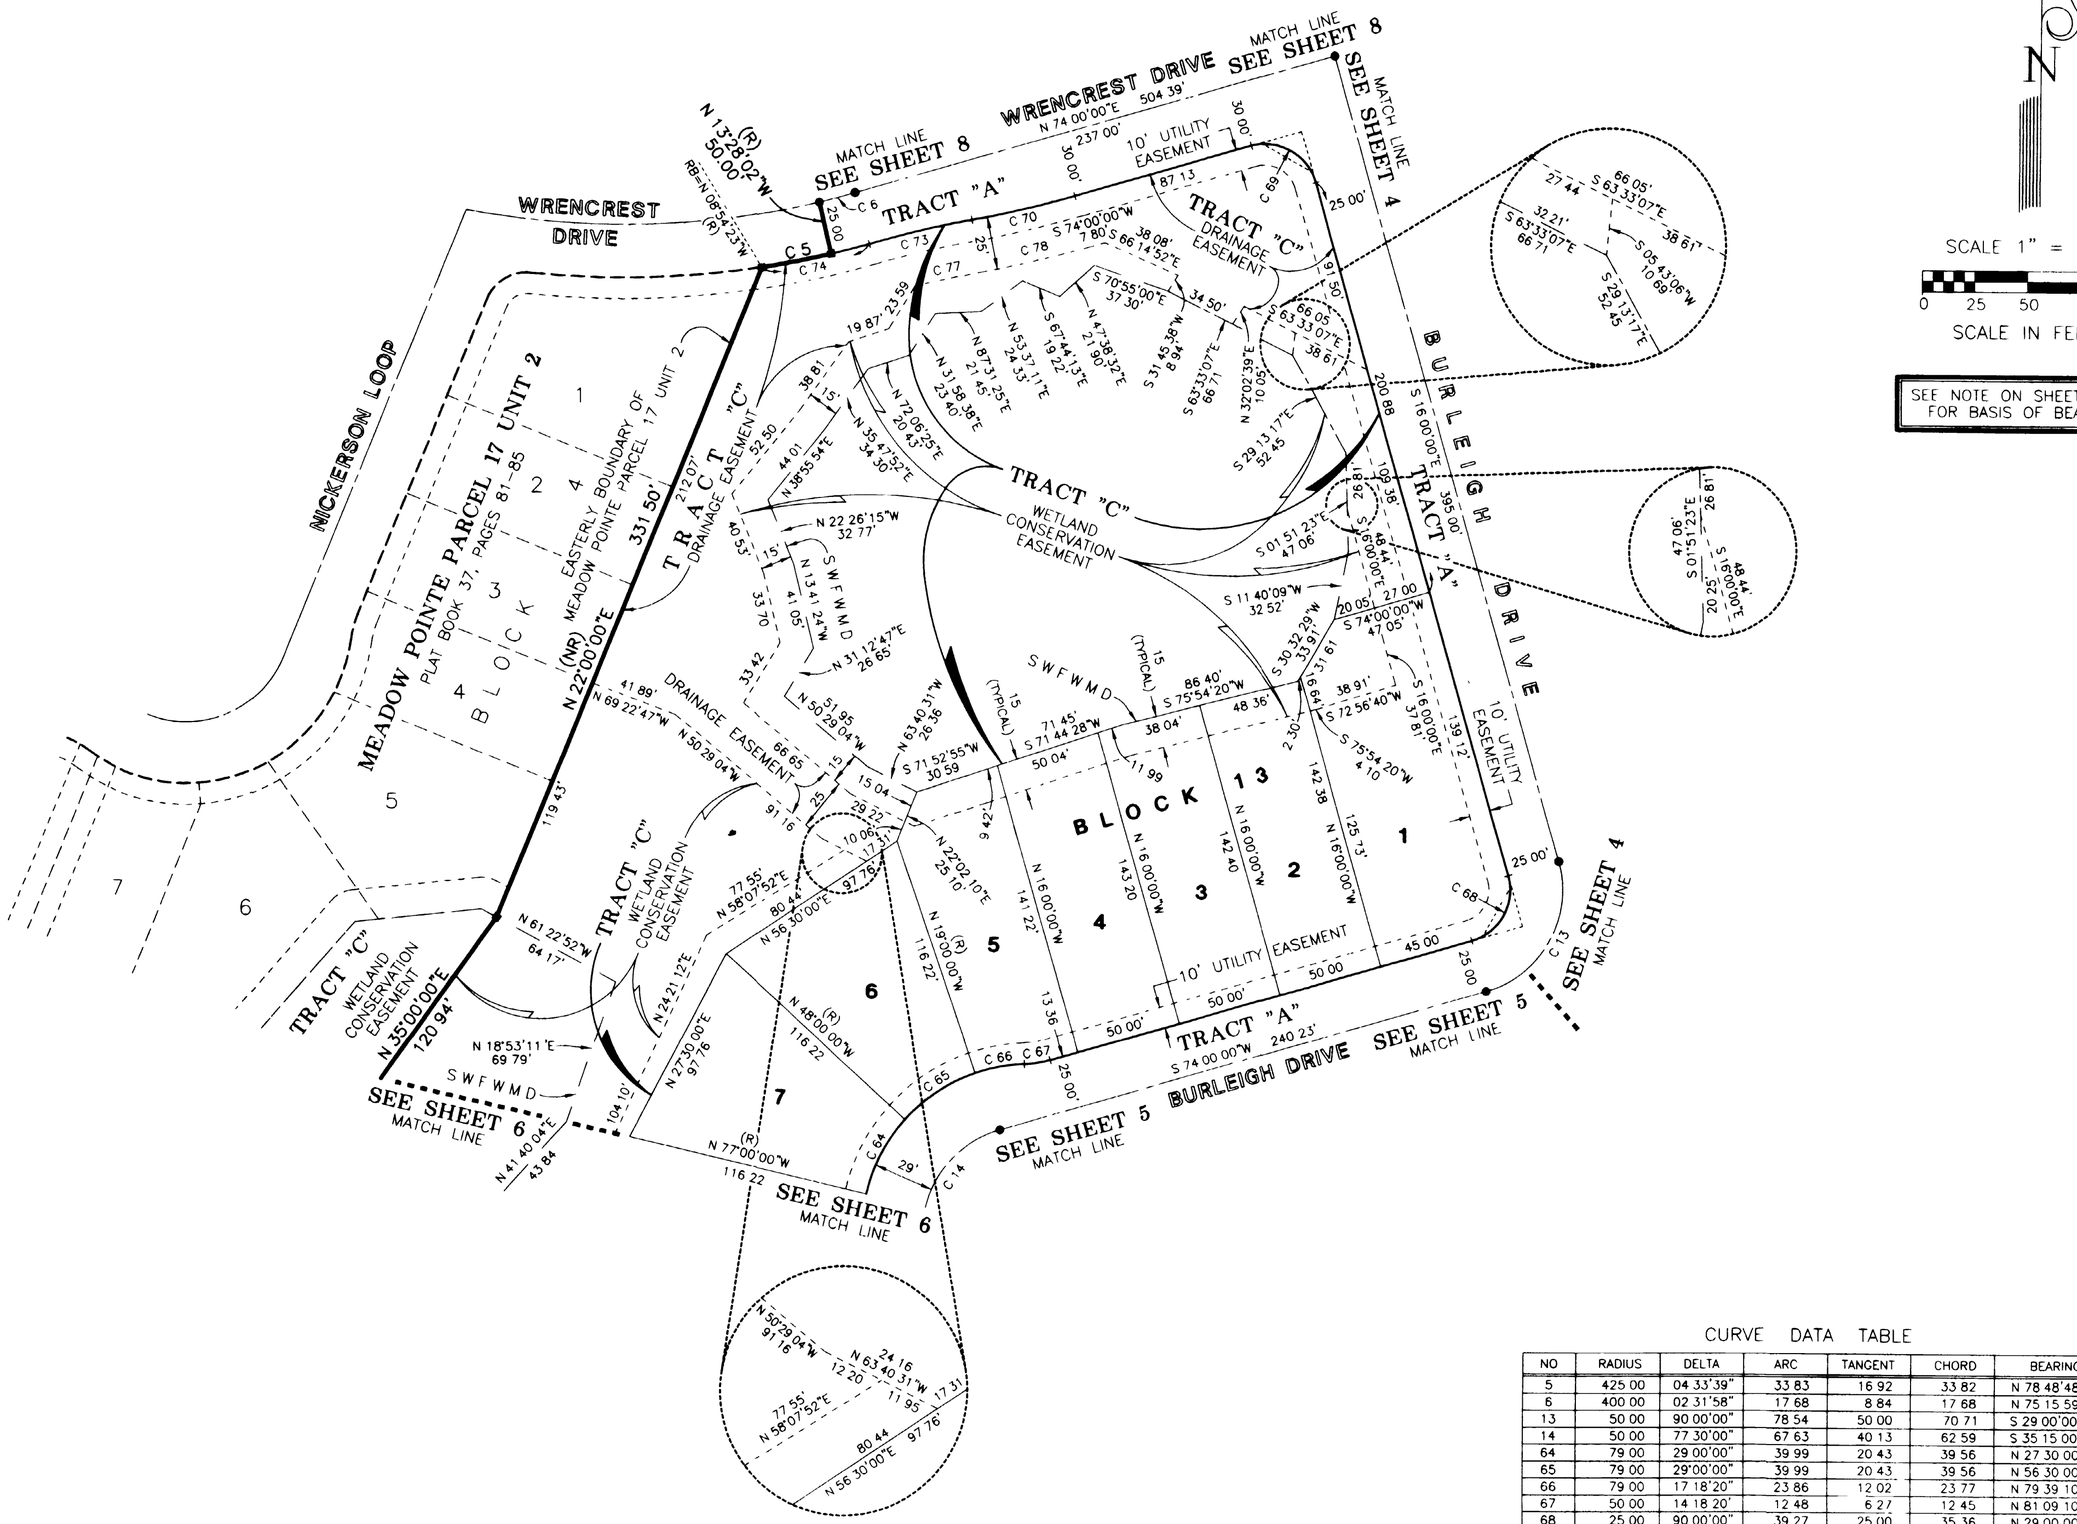

CURVE DATA TABLE

NO	RADIUS	DELTA	ARC	TANGENT	CHORD	BEARING
5	425 00	04 33'39"	33 83	16 92	33 82	N 78 48'48"E
6	400 00	02 31'58"	17 68	8 84	17 68	N 75 15 59 'E
13	50 00	90 00'00"	78 54	50 00	70 71	S 29 00'00"W
14	50 00	77 30'00"	67 63	40 13	62 59	S 35 15 00 W
64	79 00	29 00'00"	39 99	20 43	39 56	N 27 30 00"E
65	79 00	29'00'00"	39 99	20 43	39 56	N 56 30 00"E
66	79 00	17 18'20"	23 86	12 02	23 77	N 79 39 10 E
67	50 00	14 18 20'	12 48	6 27	12 45	N 81 09 10 E
68	25 00	90 00'00"	39 27	25 00	35 36	N 29 00 00 E
69	25 00	90 00 00'	39 27	25 00	35 36	N 61 00 00 W
70	500 00	05'43 55	50 02	25 03	50 00	S 76'51 58 'W
73	500 00	05 43'55"	50 02	25 03	50 00	S 76 51'58"W
74	425 00	07'05 37"	52 62	26 34	52 58	S 77 32'49"W
77	475 00	03'50'57"	31 91	15 96	31 91	N 77'48'26"E
78	525 00	05'43'55"	52 52	26 28	52 50	N 76 51'58"E

LEGEND

1 Symbol ● indicates (P R M) Permanent Reference Monument - LB148, Unless otherwise noted
2 Symbol ⊕ indicates (P R M) Offset Permanent Reference Monument - LB148, Unless otherwise noted
3 Symbol ◆ indicates (P C P) Permanent Control Point LB148 (See Sheet No 2 for P C P Reference Diagram)
4 (R) indicates radial line
5 (NR) indicates non-radial line
6 (RB) indicates reference bearing
7 S W F W M D - Southwest Florida Water Management District Wetland Line
8 W C E - Wetland Conservation Easement Line

NOTE SEE SHEET 2 OF 8 FOR DETAIL OF TYPICAL CLEAR SIGHT TRIANGLE FOR ALL CORNER LOTS

2212 SWANN AVENUE
TAMPA, FLORIDA 33606
(813) 253-5311
HEIDT & ASSOCIATES, INC
LICENSED BUSINESS NUMBER LB148
CIVIL ENGINEERING
LAND SURVEYING