**Meadow Pointe II Community Development District**

**Board of Supervisors**
□ John Picarelli, Chairperson
□ Robert Signoretti, Vice Chairperson
□ Chris Kluender, Assistant Secretary
□ Kyle Molder, Assistant Secretary
□ Jamie Childers, Assistant Secretary

□ Lee Graffius, District Manager
□ Lindsay Moczynski, District Counsel
□ Jerry Whited, District Engineer
□ Justin Wright, Operations Manager
□ John Khatiblou, Accountant

**Wednesday, August 5, 2026 – 6:30 p.m.**
**Regular Meeting Agenda**

**Communications Media Technology Via Zoom:**
https://us02web.zoom.us/j/4527478885?pwd=SWJycEJVU1VjSmVvSWRVeDJlcWIrZz09&omn=87393916259
**Meeting ID: 452 747 8885 Passcode: 6DfetC**
**Call In #: 1-929-205-6099**

1. **Call to Order**
2. **Roll Call**
3. **Pledge of Allegiance/Moment of Silence for our Fallen Service Members and First Responders**
4. **Additions or Corrections to the Agenda**
5. **Landscaping report from Juniper**
6. **Audience comments**
7. **District Manager Report**
   **A.** Discussion on Advertising the District
8. **District Engineer Report**
   **A.** Discussion of Engineer report
   **B.** Discussion on new cost and floor plans for Building from meeting
   **C.** Items and contracts to be voted on that were received
9. **District Counsel Report**
   **A.**Wrencrest Appeal Status
   **B.** Update on Morningside/Deer run sidewalks
10. **Consent Agenda**
    **A.** DRVC Violation log/pictures
11. **Architectural Review Discussion Items**
12. **Government/Community Updates**
    **A.** Community Representative Update
    i. Update on off duty Pasco County Sheriff Officer
    **B.** Event Planning Representative/ Supervisor Jamie Childers
    i. Next Event Update
13. **Items to approve/disapprove/discuss**
    **A.** Discussion on extending the landscaping
14. **Operations Manager Report**
    **A.** Update on Easement Issue and Drainpipe
15. **Audience Comments**
16. **Supervisor Comments**
17. **Adjournment**

**Management**
Inframark Management Services
2005 Pan Am Circle Ste 300
Tampa, Florida 33607

**Meeting Location**
Meadow Pointe II Clubhouse
30051 County Line Road
(813)-991-5016

**Board Workshop**
**Agenda Items for Board Discussion**
**(No Motions/ Votes Accepted. Board Discussions Only)**

1. **Call to Order**
2. **Items for Discussion**
   **A.** Discussion on Amenities Rules
   **B.** Discussion on new Deed Restrictions being revised
3. **Adjournment**

The next CDD Meeting is scheduled for Wednesday, August 19, 2026, at 6:30 p.m.

NEW COMMUNITY BUILDING AND FACILITIES MAINTENCE AND STORAGE BUILDING

# MEADOW POINTE II COMMUNITY BLDG.

MANSFIELD BLVD & COUNTY LINE RD - SE CORNER, WESLEY CHAPEL, PASCO COUNTY, FLORIDA 33543

## MEADOW POINTE II COMMUNITY DEVELOPMENT DISTRICT

WESLEY CHAPEL, PASCO COUNTY, FLORIDA 33543


ARCHITECT

RENKER EICH PARKS ARCHITECTS INC.

1609 Dr. Martin Luther King Jr. Street North
St. Petersburg, Florida 33704
(t) 727.821.2986
www.reparch.com


REPA PROJECT NO.: 2421.01

INDEX OF DRAWINGS


I GENERAL
A0.0 COVER
GA1.0 GENERAL ARCHITECTURAL

II ARCHITECTURAL
DA1.0 EXISTING SITE PLAN
A1.0 SITE PLAN
A1.1 FIRST FLOOR PLANS
A2.1 ROOF PLANS
A3.1 COMMUNITY HALL EXTERIOR ELEVATIONS
A3.2 COMMUNITY HALL EXTERIOR ELEVATIONS
A3.3 MAINTENANCE BUILDING EXTERIOR ELEVATIONS
A7.1 MEETING HALL REFLECTED CEILING PLANS
A7.2 MAINTENANCE BLDG. REFLECTED CEILING PLANS


DATE: 07/02/2026

SCHEMATIC DESIGN

## ARCHITECTURAL ABBREVIATIONS

| | |
|---|---|
| AB | ANCHOR BOLT |
| ACOUST | ACOUSTICAL |
| ADJ | ADJUSTABLE |
| AFC | ABOVE FINISHED CEILING |
| AFF | ABOVE FINISH FLOOR |
| AHU | AIR HANDLING UNIT |
| ALT | ALTERNATE |
| ALUM | ALUMINUM |
| ANOD | ANODIZED |
| AP | ACCESS PANEL |
| APPROX | APPROXIMATE |
| ARCH | ARCHITECTURAL |
| AT | ACOUSTICAL TILE |
| BD | BOARD |
| BFE | BASE FLOOD ELEVATION |
| BLDG | BUILDING |
| BM | BEAM |
| BOT | BOTTOM |
| BUR | BUILT-UP ROOFING |
| C.F.C.I. | CONTRACTOR FURNISHED AND CONTRACTOR INSTALLED |
| CAB | CABINET |
| CG | CORNER GUARD |
| CI | CAST IRON |
| CJ | CONTROL JOINT |
| CL | CLEAR |
| CLO | CLOSET |
| CMU | CONCRETE MASONRY UNIT |
| CNT | COUNTER |
| COL | COLUMN |
| CONC | CONCRETE |
| CONST | CONSTRUCTION |
| CONT | CONTINUOUS |
| CONTR | CONTRACTOR |
| CORR | CORRIDOR |
| CPT | CARPET |
| CT | CERAMIC TILE |
| DET | DETAIL |
| DIA | DIAMETER |
| DIAG | DIAGONAL |
| DIM | DIMENSION |
| DISP | DISPENSER |
| DN | DOWN |
| DWG | DRAWING |
| EB | EXPANSION BOLT |
| EJ | EXPANSION JOINT |
| EL | ELEVATION |
| ELEC | ELECTRICAL |
| ELEV | ELEVATION |
| EP | ELECTRICAL PANEL |
| EQ | EQUAL |
| EQUIP | EQUIPMENT |
| ETR | EXISTING TO REMAIN |
| EWC | ELECTRIC WATER COOLER |
| EX | EXISTING |
| EXP | EXPOSED |
| EXT | EXTERIOR |
| FC | FURRING CHANNEL |
| FD | FLOOR DRAIN |
| FEC | FIRE EXTINGUISHER CABINET |
| FF | FINISH FLOOR |
| FHC | FIRE HOSE CABINET |
| FIN | FINISH |
| FL | FLOOR |
| FR | FIRE RATED |
| GA | GUAGE |
| GALV | GALVANIZED |
| GC | GENERAL CONTRACTOR |
| GFRC | GLASS FIBER REINFORCED CEMENT |
| GFRG | GLASS FIBER REINFORCED GYPSUM |
| GL | GLASS |
| GR | GRADE |
| GWB | GYPSUM WALLBOARD |
| GYP | GYPSUM |
| HB | HOSE BIB |
| HT | HEIGHT |
| HVAC | HEATING, VENTILATING, & AIR CONDITIONING |
| ID | INSIDE DIAMETER |
| INSUL | INSULATION |
| INT | INTERIOR |
| JT | JOINT |
| KIT | KITCHEN |
| KW | KILOWATT |
| L | LENGTH |
| LAM | LAMINATE |
| LAV | LAVATORY |
| LF | LINEAR FEET |
| LKR | LOCKER |
| LL | LEAD LINED |
| LYR | LAYER |
| MFD | MANUFACTURED |
| MFR | MANUFACTURER |
| MH | MANHOLE |
| MIN | MINIMUM |
| MIR | MORROR |
| MISC | MISCELLANEOUS |
| MLDG | MOLDING |
| MO | MASONRY OPENING |
| MR | MOISTURE RESISTANT |
| MT | METAL THRESHOLD |
| MTD | MOUNTED |
| MTL | METAL |
| NIC | NOT IN CONTRACT |
| NOM | NOMINAL |
| NTS | NOT TO SCALE |
| OA | OVERALL |
| OC | ON CENTER |
| OD | OUTSIDE DIAMETER |
| OFCI | OWNER FURNISHED CONTRACTOR INSTALLED |
| PL | PLATE |
| PLAM | PLASTIC LAMINATE |
| PLAS | PLASTER |
| PLUMB | PLUMBING |
| PLWD | PLYWOOD |
| PNT | PAINT |
| PT | PRESSURE TREATED |
| PTD | PAPER TOWEL DISPENSER |
| PVC | POLYVINYL CHLORIDE |
| QT | QUARRY TILE |
| R | RADIUS |
| RCP | REINFORCED CONCRETE PIPE |
| RD | ROOF DRAIN |
| REC | RECEPTACLE |
| REF | REFRIGERATOR |
| REG | REGLET |
| REINF | REINFORCED |
| REQD | REQUIRED |
| RJ | REVEAL JOINT |
| RM | ROOM |
| RO | ROUGH OPENING |
| SCHD | SCHEDULE |
| SCRN | SCREEN |
| SEC | SECTION |
| SH | SHELF |
| SHT | SHEET |
| SIM | SIMILAR |
| SP | SPACE |
| SPECS | SPECIFICATIONS |
| SS | STAINLESS STEEL |
| STL | STEEL |
| STOR | STORAGE |
| STRUC | STRUCTURAL |
| SUSP | SUSPENDED |
| TB | TOGGLE BOLT |
| TC | TOILET COMPARTMENT |
| TEL | TELEPHONE |
| TEMP | TEMPERATURE |
| TPD | TOILET PAPER DISPENSER |
| TYP | TYPICAL |
| UC | UNDERCOUNTER |
| UNO | UNLESS NOTED OTHERWISE |
| UTIL | UTILITY |
| VB | VINYL BASE |
| VERT | VERTICAL |
| VEST | VESTIBULE |
| VIF | VERIFY IN FIELD |
| VTR | VENT THROUGH ROOF |
| VWC | VINYL WALLCOVERING |
| W | WIDTH |
| W/ | WITH |
| WC | WATER CLOSET |
| WD | WOOD |
| WP | WEATHER PROOF |
| WWF | WELDED WIRE FABRIC |

## GENERAL PROJECT NOTES

A ISOLATE ALL DISSIMILAR MATERIALS, TYP.

B SEALERS TO BE COMPATIBLE WHERE IN CONTACT W/ ONE ANOTHER AND OTHER MATERIALS.

C CONTRACTOR SHALL HAVE PORTABLE FIRE EXTINGUISHER ON SITE AND AVAILABLE AT ALL TIMES.

D CONTRACTOR SHALL OBTAIN ALL PERMITS NECESSARY TO PERFORM THEIR PROJECT. ALL PERMIT FEES ARE BY OTHERS.

E DO NOT SCALE DRAWINGS, IF DIMENSIONS ARE IN QUESTION THE CONTRACTOR SHALL BE RESPONSIBLE FOR OBTAINING CLARIFICATION FROM THE ARCHITECT PRIOR TO CONTINUATION OF WORK.

## DIMENSION NOTES

1 ALL DOOR FRAME OPENINGS IN MASONRY SHALL BE 3'-4" MO UNO


2 ALL DIMENSION STRINGS SHALL BE TO FACE OF WALL STRUCTURE (IE CMU, MTL STUD FRAMING)

3 DIMENSION STRINGS NOTED AS CLEAR SHALL BE TO FACE OF FINISHED WALL OR PARTITION (IE FACE OF GWB, PLASTER, OR TILE)

4 DOOR JAMB RETURNS IN MASONRY WALLS TO HINGE SIDE SHALL BE 8" NOM UNO

5 DOOR JAMB RETURNS IN MTL FRAMING WALLS TO HINGE SIDE SHALL BE 4" NOM UNO

## DRAWING LEGEND

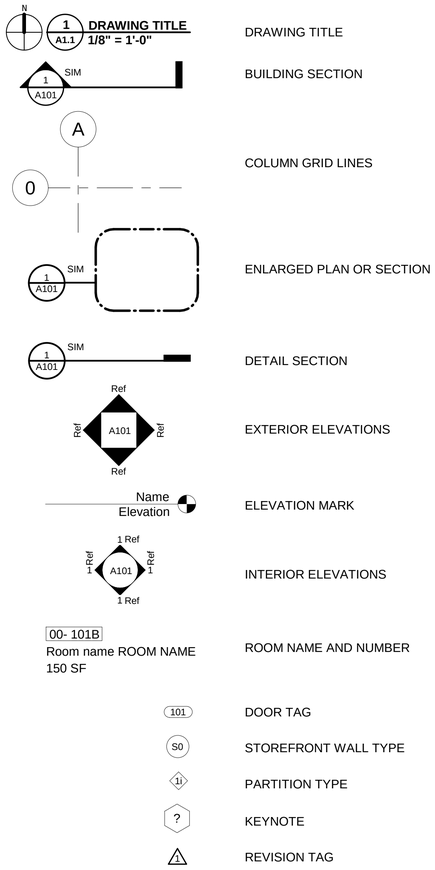


DRAWING TITLE

BUILDING SECTION

COLUMN GRID LINES

ENLARGED PLAN OR SECTION

DETAIL SECTION

EXTERIOR ELEVATIONS

ELEVATION MARK

INTERIOR ELEVATIONS

ROOM NAME AND NUMBER

DOOR TAG

STOREFRONT WALL TYPE

PARTITION TYPE

KEYNOTE

REVISION TAG

## BUILDING CODE SUMMARY

PROJECT DESCRIPTION:

BUILDING AREA (GROSS):

## OCCUPANCY CLASSIFICATION / CONSTRUCTION TYPE:

## APPLICABLE CODES

2023 FLORIDA BUILDING CODE - BUILDING
2023 FLORIDA BUILDING CODE - EXISTING BUILDING
2023 FLORIDA BUILDING CODE - MECHANICAL
2023 FLORIDA BUILDING CODE - PLUMBING
2023 FLORIDA BUILDING CODE - FUEL GAS
2023 FLORIDA BUILDING CODE - TEST PROTOCOLS
2023 FLORIDA BUILDING CODE - ENERGY (Chapter 13)
2023 FLORIDA BUILDING CODE - ACCESSIBILITY
2023 FLORIDA FIRE PREVENTION CODE, 8th EDITION
2020 NFPA 70 NATIONAL ELECTRICAL CODE
2021 NFPA 101 LIFE SAFETY CODE




SITE LOCATION

REP
RENKER EICH PARKS ARCHITECTS

SCHEMATIC DESIGN

NEW COMMUNITY BUILDING AND FACILITIES
MAINTENCE AND STORAGE BUILDING

MEADOW POINTE II COMMUNITY BLDG.
MANSFIELD BLVD & COUNTY LINE RD - SE CORNER, WESLEY CHAPEL, PASCO COUNTY, FLORIDA 33543

MEADOW POINTE II COMMUNITY DEVELOPMENT DISTRICT
WESLEY CHAPEL, PASCO COUNTY, FLORIDA 33543

**PROJECT NO.:2421.01**
**DATE: 06/24/2026**
**DRAWN BY:YS**
**REVISIONS:**

**SHEET TITLE:**
GENERAL
ARCHITECTURAL

**SHEET NO.:**
GA1.0

7/2/2026 11:55:49 AM
Autodesk Docs://2421.01 MPII Community Hall & Facilities Maintenance/2421.01 - Meadow Pointe II Community Bldg.rvt

## SPECIFIC NOTES




N

1 DA1.0 **EXISTING SITE PLAN**
**1" = 30'-0"**

SCHEMATIC DESIGN

REP
RENKER EICH PARKS ARCHITECTS

NEW COMMUNITY BUILDING AND FACILITIES
MAINTENCE AND STORAGE BUILDING

# MEADOW POINTE II COMMUNITY BLDG.

MANSFIELD BLVD & COUNTY LINE RD - SE CORNER, WESLEY CHAPEL, PASCO COUNTY, FLORIDA 33543

MEADOW POINTE II COMMUNITY DEVELOPMENT DISTRICT
WESLEY CHAPEL, PASCO COUNTY, FLORIDA 33543


**PROJECT NO.:2421.01**
**DATE: 06/24/2026**
**DRAWN BY:YS**
**REVISIONS:**

**SHEET TITLE:**
EXISTING SITE PLAN

**SHEET NO.:**
DA1.0

7/2/2026 11:56:00 AM
Autodesk Docs://2421.01 MPII Community Hall & Facilities Maintenance/2421.01 - Meadow Pointe II Community Bldg.rvt

## SPECIFIC NOTES

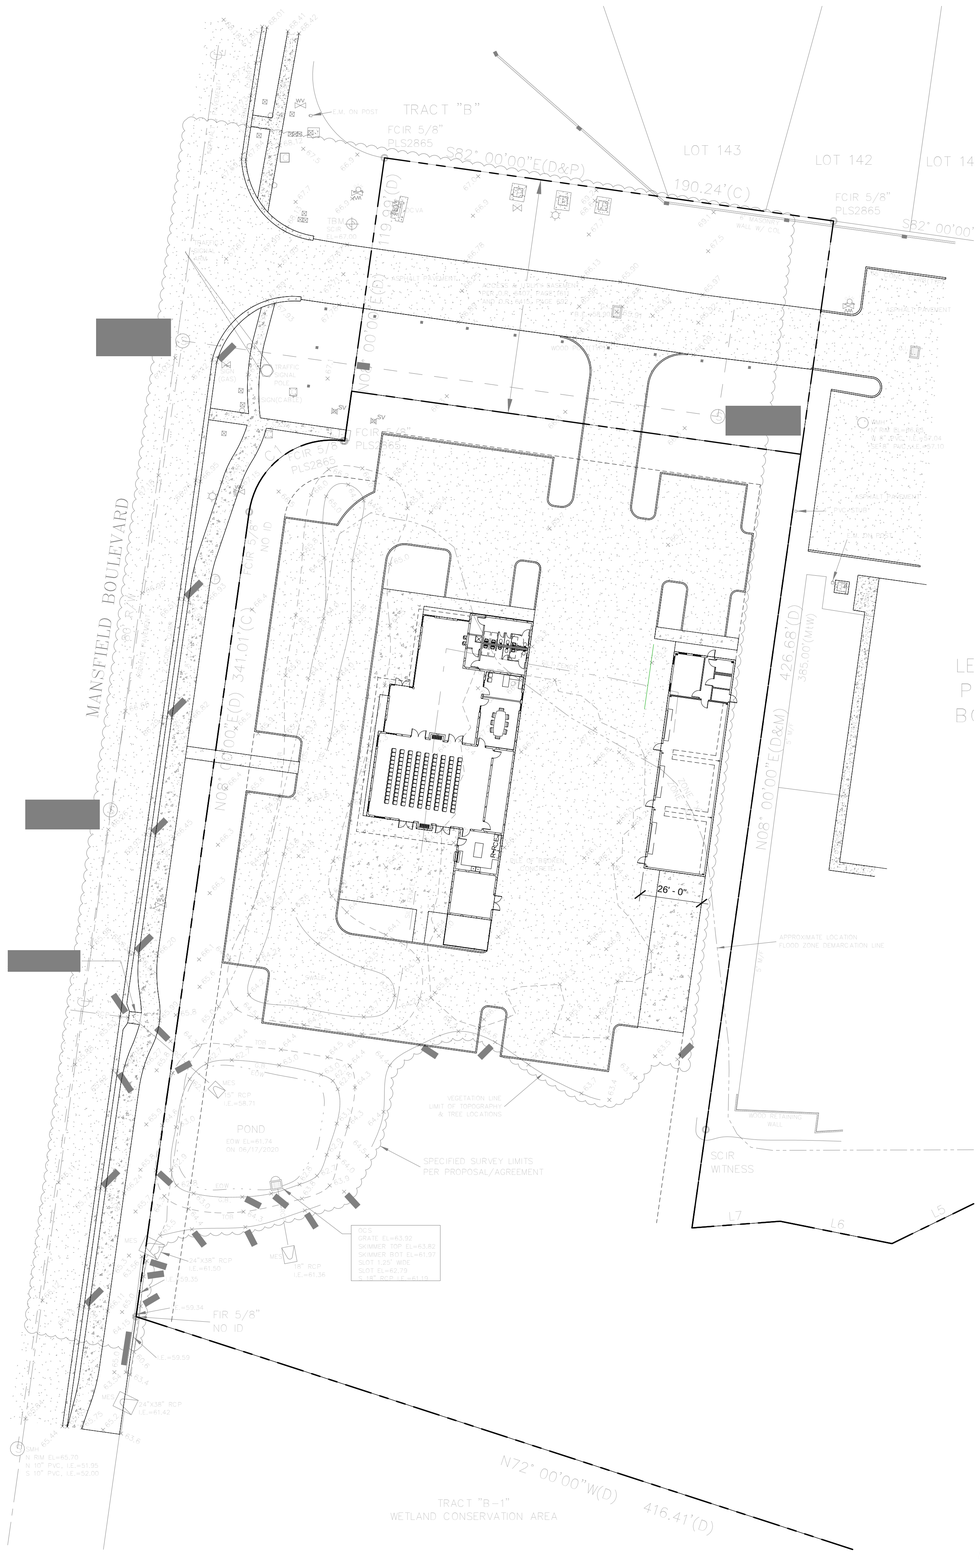


N

1 / A1.0 **SITE PLAN**
1" = 30'-0"

SCHEMATIC DESIGN

NEW COMMUNITY BUILDING AND FACILITIES
MAINTENCE AND STORAGE BUILDING

# MEADOW POINTE II COMMUNITY BLDG.

MANSFIELD BLVD & COUNTY LINE RD - SE CORNER, WESLEY CHAPEL, PASCO COUNTY, FLORIDA 33543

MEADOW POINTE II COMMUNITY DEVELOPMENT DISTRICT
WESLEY CHAPEL, PASCO COUNTY, FLORIDA 33543

**PROJECT NO.:2421.01**
**DATE: 06/24/2026**
**DRAWN BY:YS**
**REVISIONS:**

**SHEET TITLE:**
SITE PLAN


**SHEET NO.:**
A1.0


RENKER EICH PARKS ARCHITECTS




7/2/2026 2:44:53 PM
Autodesk Docs://2421.01 MPII Community Hall & Facilities Maintenance/2421.01 - Meadow Pointe II Community Bldg.rvt

## SPECIFIC NOTES

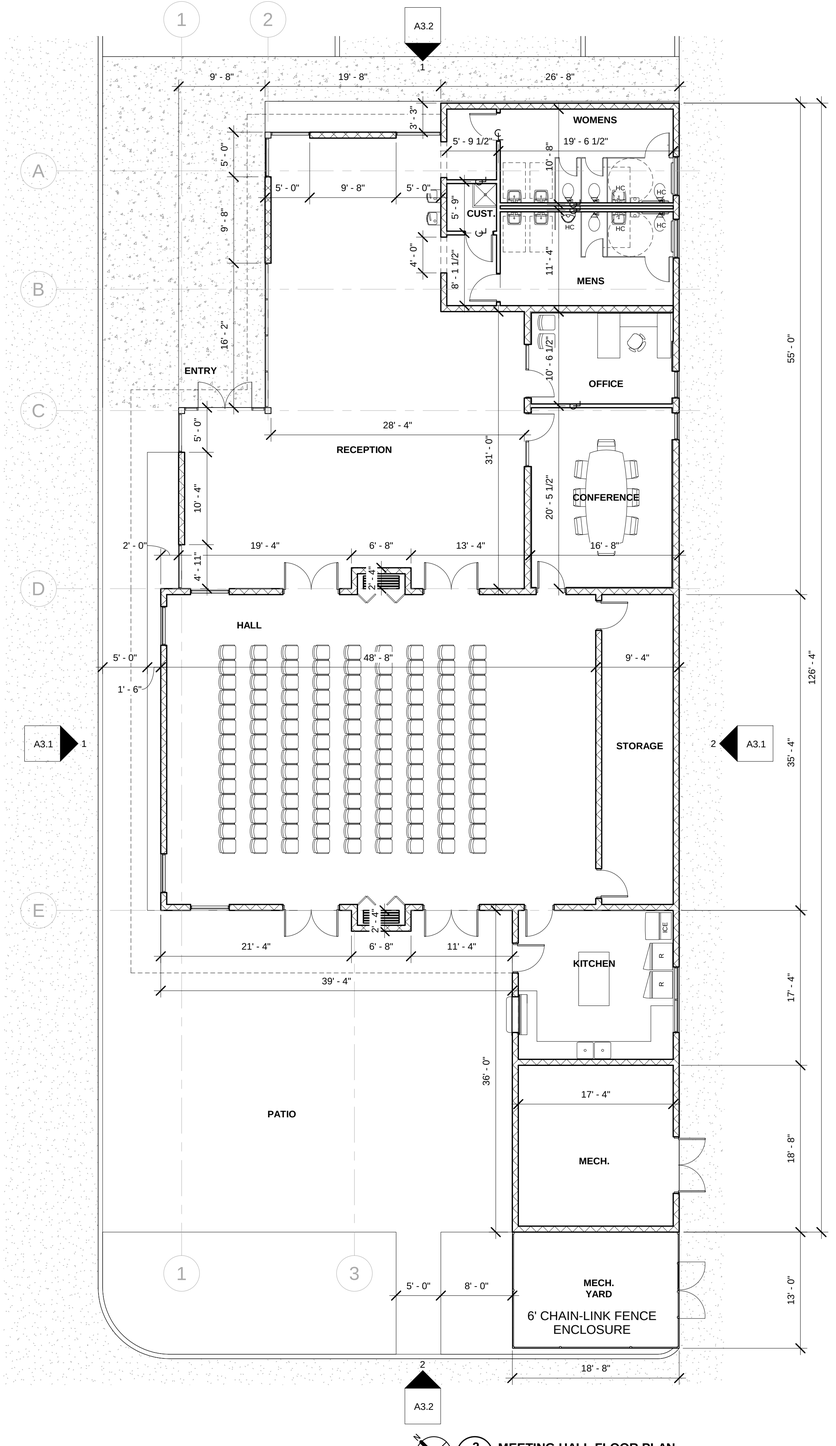


2 A1.1 **MEETING HALL FLOOR PLAN**
**1/8" = 1'-0"**

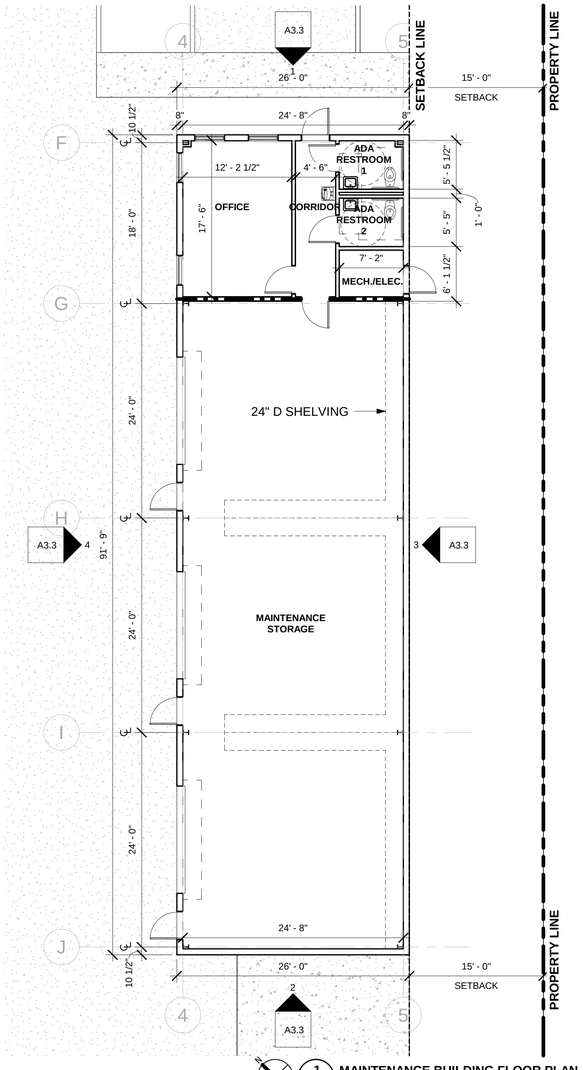


1 A1.1 **MAINTENANCE BUILDING FLOOR PLAN**
**1/8" = 1'-0"**

SCHEMATIC DESIGN

NEW COMMUNITY BUILDING AND FACILITIES
MAINTENCE AND STORAGE BUILDING

# MEADOW POINTE II COMMUNITY BLDG.

MANSFIELD BLVD & COUNTY LINE RD - SE CORNER, WESLEY CHAPEL, PASCO COUNTY, FLORIDA 33543

MEADOW POINTE II COMMUNITY DEVELOPMENT DISTRICT
WESLEY CHAPEL, PASCO COUNTY, FLORIDA 33543


**PROJECT NO.:2421.01**
**DATE: 06/24/2026**
**DRAWN BY:YS**
**REVISIONS:**

**SHEET TITLE:**
FIRST FLOOR PLANS


**SHEET NO.:**
A1.1

7/2/2026 2:45:00 PM
Autodesk Docs://2421.01 MPII Community Hall & Facilities Maintenance/2421.01 - Meadow Pointe II Community Bldg.rvt

## SPECIFIC NOTES

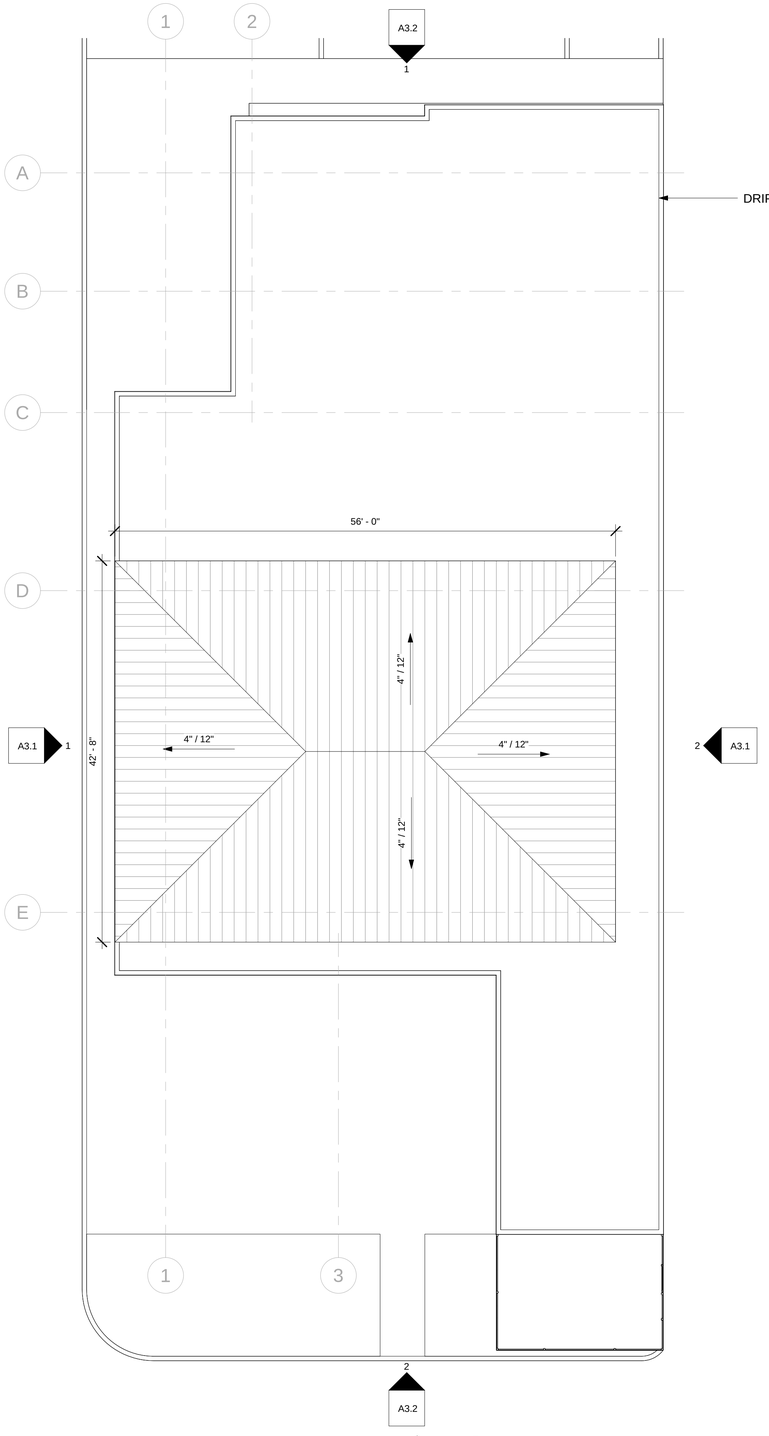


2 A2.1 **MEETIN HALL ROOF PLAN**
**1/8" = 1'-0"**

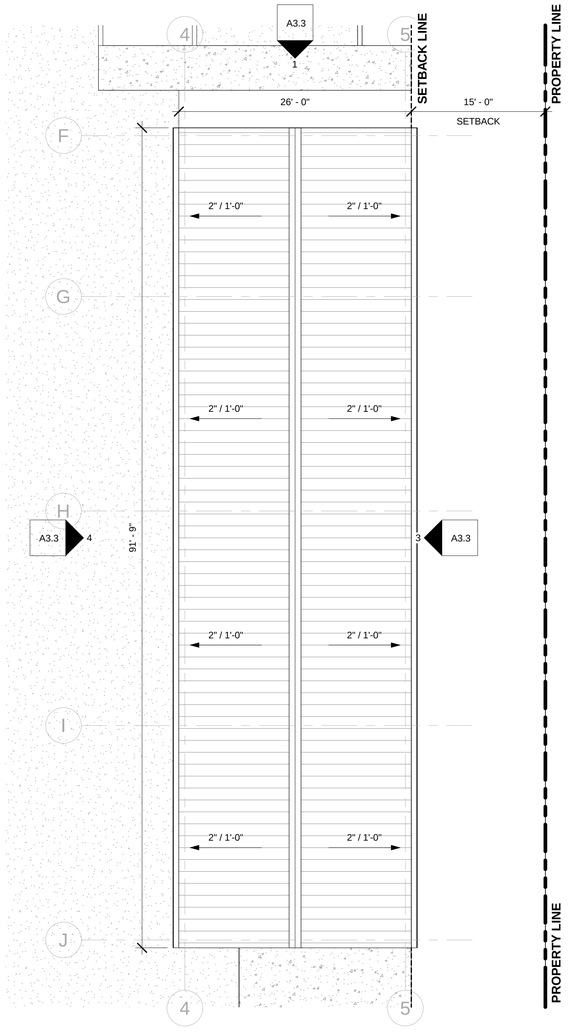


1 A2.1 **MAINTENANCE BUILDING ROOF PLAN**
**1/8" = 1'-0"**


REP
RENKER EICH PARKS ARCHITECTS


SCHEMATIC DESIGN

NEW COMMUNITY BUILDING AND FACILITIES
MAINTENCE AND STORAGE BUILDING

# MEADOW POINTE II COMMUNITY BLDG.

MANSFIELD BLVD & COUNTY LINE RD - SE CORNER, WESLEY CHAPEL, PASCO COUNTY, FLORIDA 33543


MEADOW POINTE II COMMUNITY DEVELOPMENT DISTRICT
WESLEY CHAPEL, PASCO COUNTY, FLORIDA 33543

**PROJECT NO.:2421.01**
**DATE: 06/24/2026**
**DRAWN BY:YS**
**REVISIONS:**


**SHEET TITLE:**
ROOF PLANS

**SHEET NO.:**
A2.1


7/2/2026 2:45:10 PM
Autodesk Docs://2421.01 MPII Community Hall & Facilities Maintenance/2421.01 - Meadow Pointe II Community Bldg.rvt

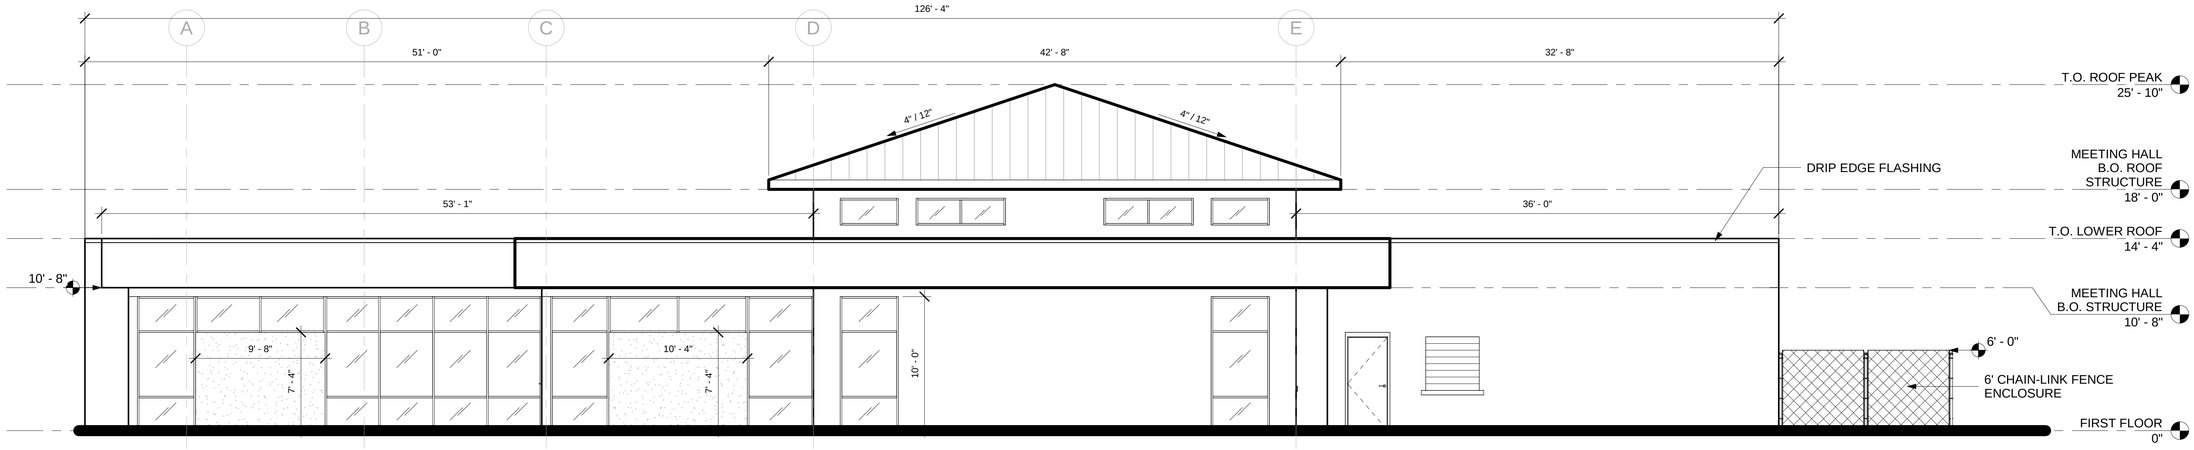


1 A3.1 **MEETING HALL - WEST ELEVATION**
**3/16" = 1'-0"**

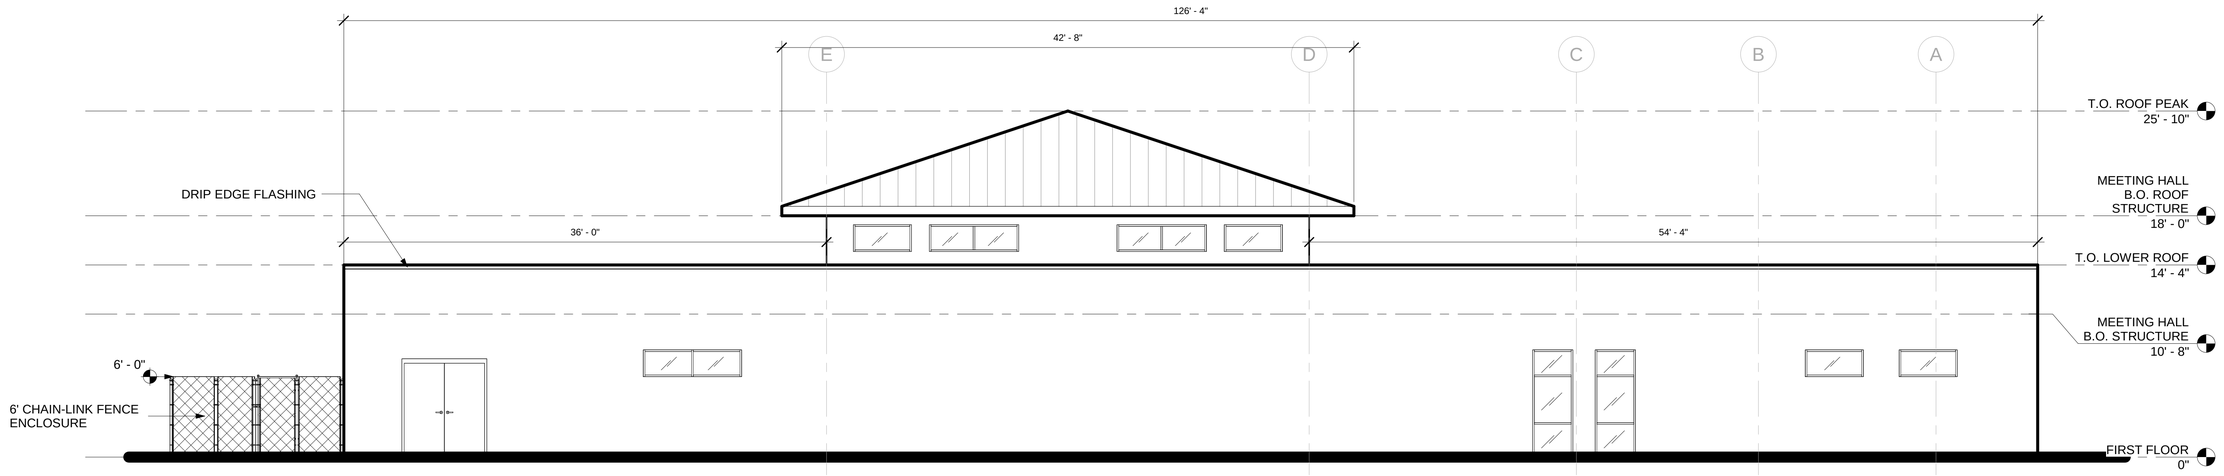


2 A3.1 **MEETING HALL - EAST ELEVATION**
**3/16" = 1'-0"**

## SPECIFIC NOTES

REP
RENKER EICH PARKS
ARCHITECTS

SCHEMATIC DESIGN

NEW COMMUNITY BUILDING AND FACILITIES
MAINTENCE AND STORAGE BUILDING

MEADOW POINTE II COMMUNITY BLDG.

MANSFIELD BLVD & COUNTY LINE RD - SE CORNER, WESLEY CHAPEL, PASCO COUNTY, FLORIDA 33543

MEADOW POINTE II COMMUNITY DEVELOPMENT DISTRICT
WESLEY CHAPEL, PASCO COUNTY, FLORIDA 33543


**PROJECT NO.:2421.01**
**DATE: 06/24/2026**
**DRAWN BY:YS**
**REVISIONS:**

**SHEET TITLE:**
COMMUNITY HALL EXTERIOR ELEVATIONS


**SHEET NO.:**
A3.1

7/2/2026 2:45:24 PM
Autodesk Docs://2421.01 MPII Community Hall & Facilities Maintenance/2421.01 - Meadow Pointe II Community Bldg.rvt

## SPECIFIC NOTES

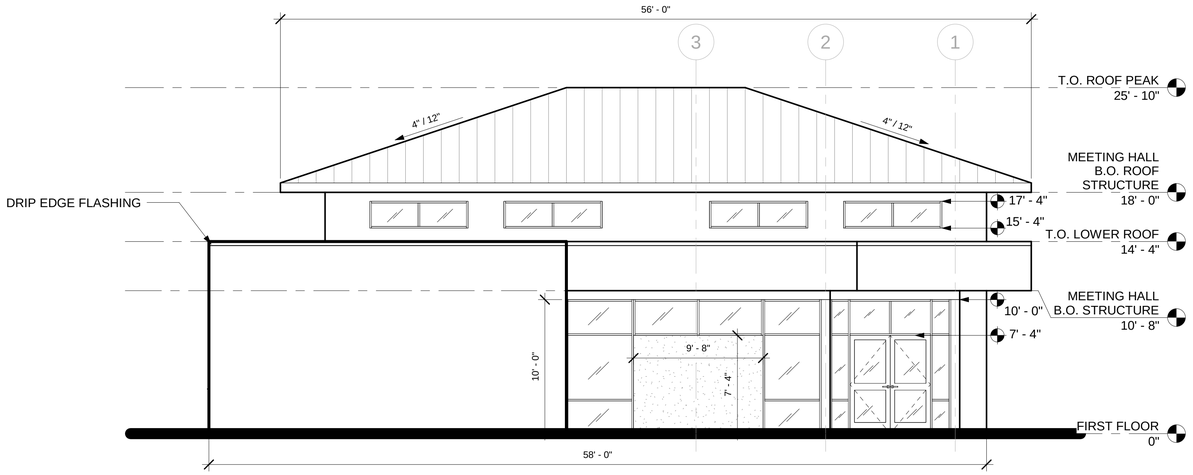


1 A3.2 **MEETING HALL - NORTH ELEVATION**
**3/16" = 1'-0"**

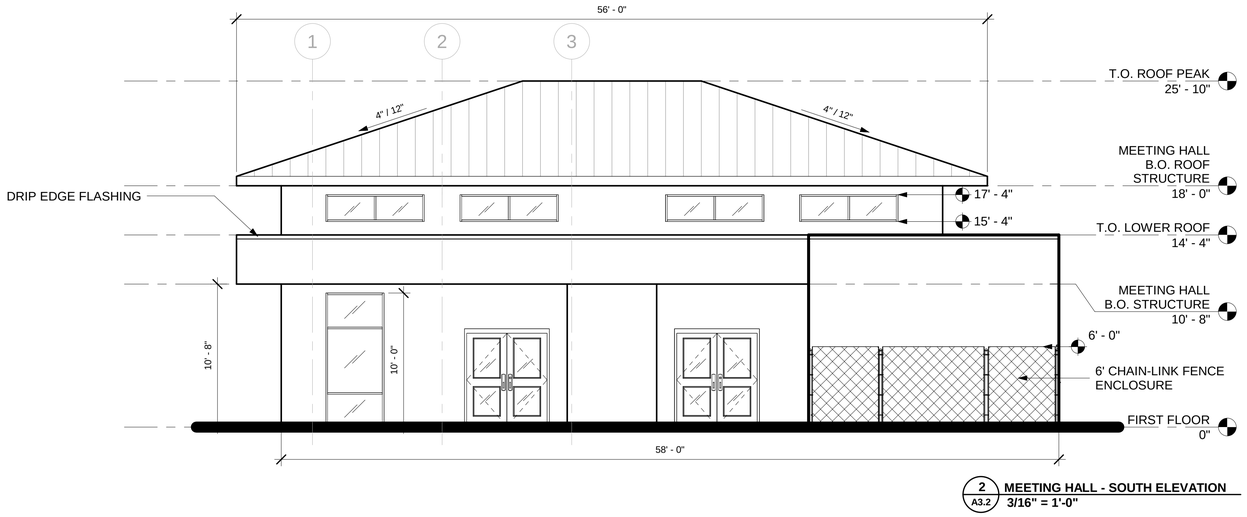


2 A3.2 **MEETING HALL - SOUTH ELEVATION**
**3/16" = 1'-0"**

REP
RENKER EICH PARKS ARCHITECTS

SCHEMATIC DESIGN

NEW COMMUNITY BUILDING AND FACILITIES
MAINTENCE AND STORAGE BUILDING

**MEADOW POINTE II COMMUNITY BLDG.**

MANSFIELD BLVD & COUNTY LINE RD - SE CORNER, WESLEY CHAPEL, PASCO COUNTY, FLORIDA 33543


MEADOW POINTE II COMMUNITY DEVELOPMENT DISTRICT
WESLEY CHAPEL, PASCO COUNTY, FLORIDA 33543

**PROJECT NO.:2421.01**
**DATE: 06/24/2026**
**DRAWN BY:YS**
**REVISIONS:**


**SHEET TITLE:**
COMMUNITY HALL EXTERIOR ELEVATIONS

**SHEET NO.:**
A3.2


7/2/2026 2:46:21 PM
Autodesk Docs://2421.01 MPII Community Hall & Facilities Maintenance/2421.01 - Meadow Pointe II Community Bldg.rvt

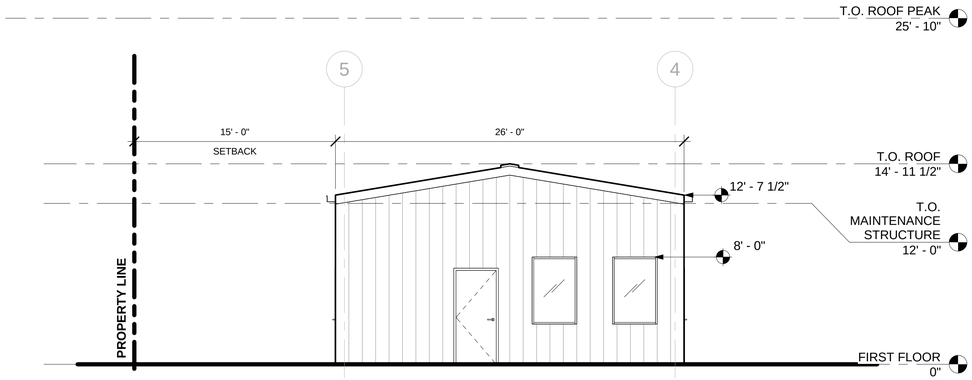



1 A3.3 **MAINTENANCE BUILDING - NORTH ELEVATION**
**3/16" = 1'-0"**

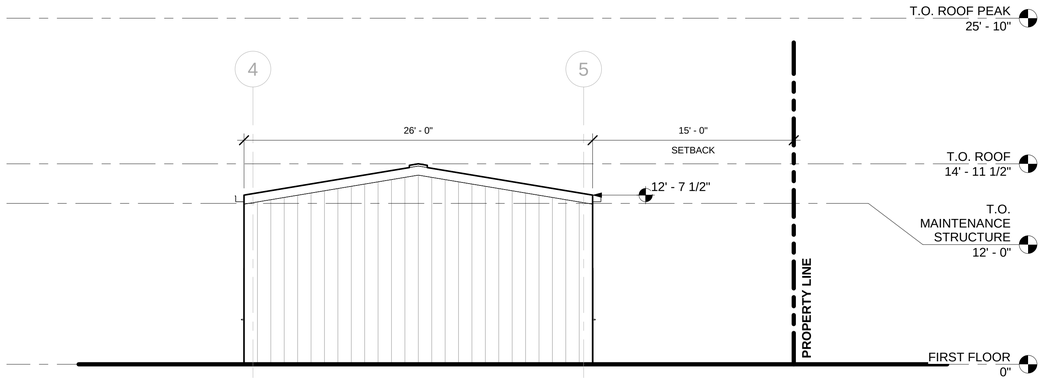


2 A3.3 **MAINTENANCE BUILDING - SOUTH ELEVATION**
**3/16" = 1'-0"**

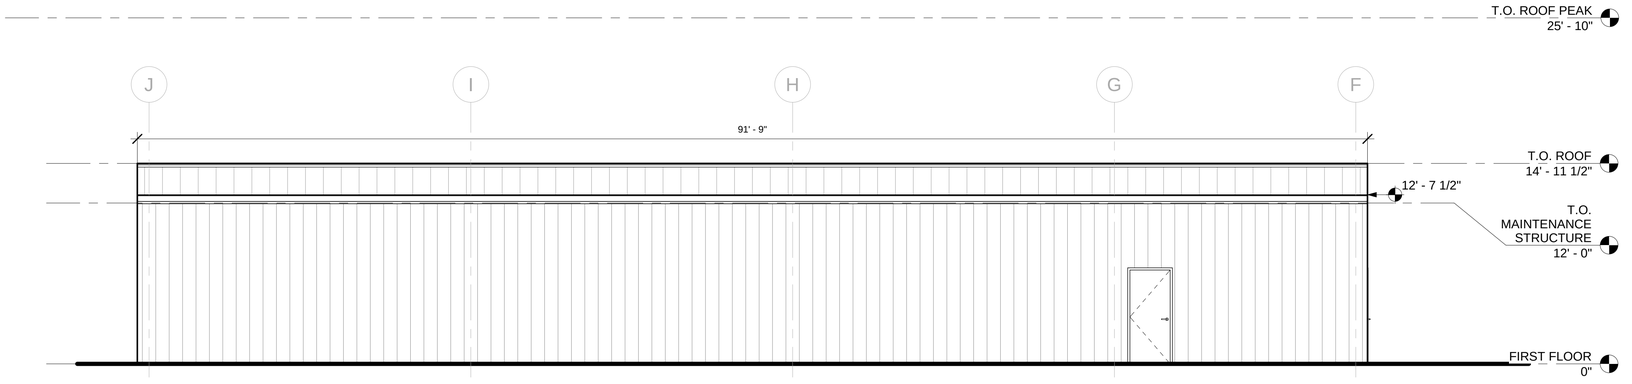


3 A3.3 **MAINTENANCE BUILDING - EAST ELEVATION**
**3/16" = 1'-0"**

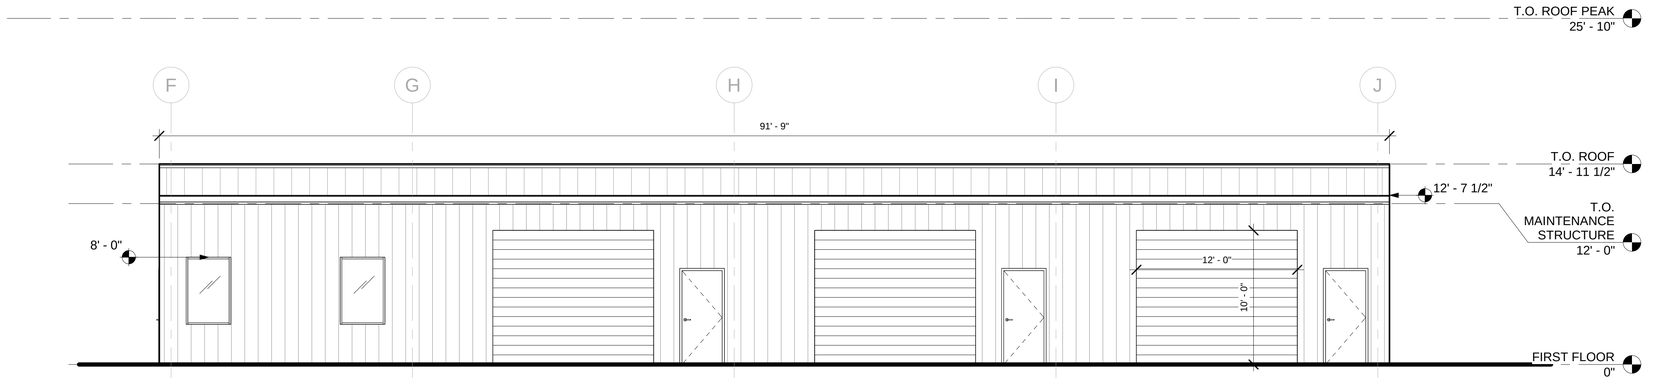


4 A3.3 **MAINTENANCE BUILDING - WEST ELEVATION**
**3/16" = 1'-0"**

## SPECIFIC NOTES

SCHEMATIC DESIGN

NEW COMMUNITY BUILDING AND FACILITIES
MAINTENCE AND STORAGE BUILDING

# MEADOW POINTE II COMMUNITY BLDG.

MANSFIELD BLVD & COUNTY LINE RD - SE CORNER, WESLEY CHAPEL, PASCO COUNTY, FLORIDA 33543

MEADOW POINTE II COMMUNITY DEVELOPMENT DISTRICT
WESLEY CHAPEL, PASCO COUNTY, FLORIDA 33543

REP
RENKER EICH PARKS ARCHITECTS


**PROJECT NO.:2421.01**
**DATE: 06/24/2026**
**DRAWN BY:YS**
**REVISIONS:**

**SHEET TITLE:**
MAINTENANCE BUILDING EXTERIOR ELEVATIONS

**SHEET NO.:**
A3.3

7/2/2026 11:57:45 AM
Autodesk Docs://2421.01 MPII Community Hall & Facilities Maintenance/2421.01 - Meadow Pointe II Community Bldg.rvt

## SPECIFIC NOTES

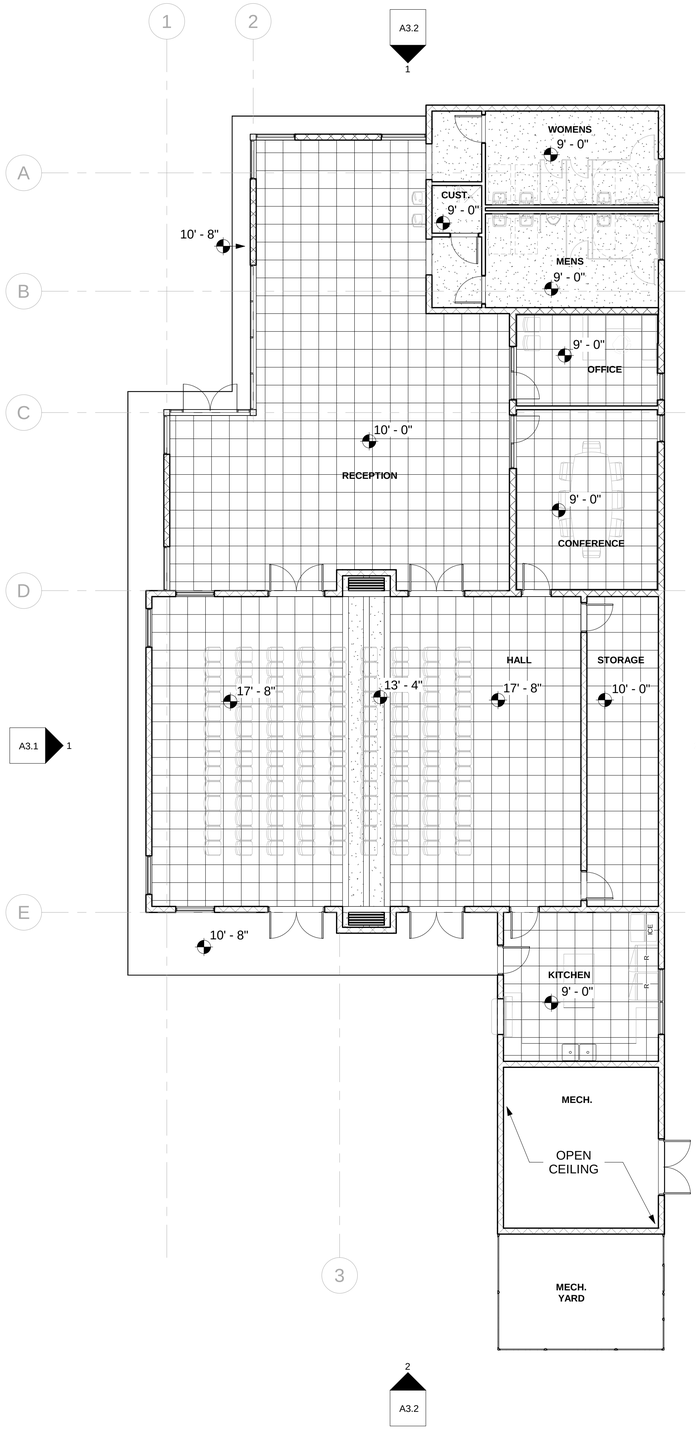


1 A7.1 **MEETING HALL LOW CEILING**
**1/8" = 1'-0"**

## RCP LEGEND

- 2X2 LED FIXTURE
- 1X4 LINEAR LED FIXTURE
- LED UTILITY STRIP LIGHT
- LED CAN LIGHT
- ACOUSTIC PANEL CEILING SYSTEM
- GWB CEILING
- STUCCO CEILING
- METAL CANOPY
- SPEAKER
- SOFFIT VENT
- SPRINKLER

REP
RENKER EICH PARKS ARCHITECTS

SCHEMATIC DESIGN

NEW COMMUNITY BUILDING AND FACILITIES
MAINTENCE AND STORAGE BUILDING

# MEADOW POINTE II COMMUNITY BLDG.

MANSFIELD BLVD & COUNTY LINE RD - SE CORNER, WESLEY CHAPEL, PASCO COUNTY, FLORIDA 33543


MEADOW POINTE II COMMUNITY DEVELOPMENT DISTRICT
WESLEY CHAPEL, PASCO COUNTY, FLORIDA 33543

**PROJECT NO.:2421.01**
**DATE: 06/24/2026**
**DRAWN BY:YS**
**REVISIONS:**

**SHEET TITLE:**
MEETING HALL REFLECTED CEILING PLANS

**SHEET NO.:**
A7.1

7/2/2026 11:57:57 AM
Autodesk Docs://2421.01 MPII Community Hall & Facilities Maintenance/2421.01 - Meadow Pointe II Community Bldg.rvt

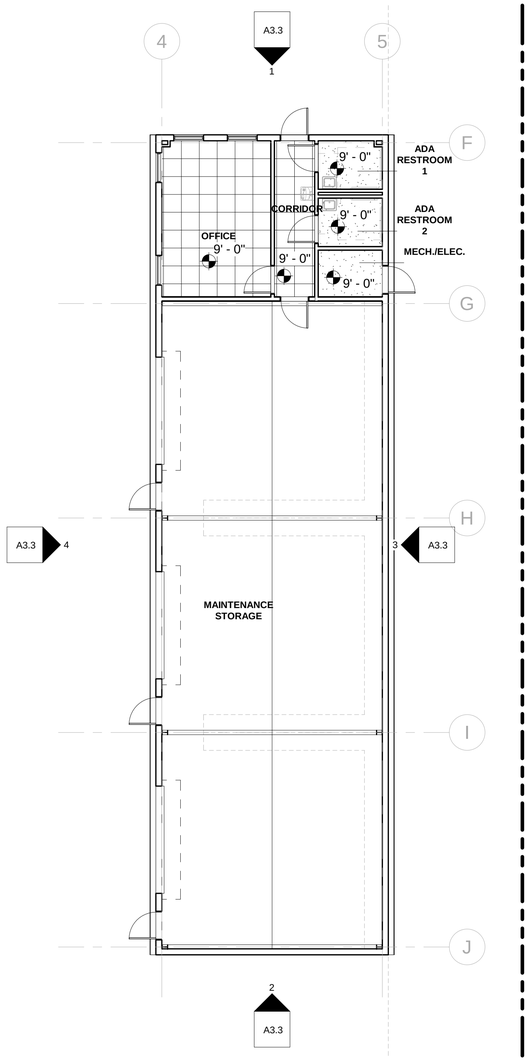


2 / A7.2 MAINTENANCE BUILDING FIRST FLOOR REFLECTED CEILING PLAN
1/8" = 1'-0"

## SPECIFIC NOTES

## RCP LEGEND

- 2X2 LED FIXTURE
- 1X4 LINEAR LED FIXTURE
- LED UTILITY STRIP LIGHT
- LED CAN LIGHT
- ACOUSTIC PANEL CEILING SYSTEM
- GWB CEILING
- STUCCO CEILING
- METAL CANOPY
- SPEAKER
- SOFFIT VENT
- SPRINKLER

REP
RENKER EICH PARKS ARCHITECTS

SCHEMATIC DESIGN

NEW COMMUNITY BUILDING AND FACILITIES
MAINTENCE AND STORAGE BUILDING
MEADOW POINTE II COMMUNITY BLDG.
MANSFIELD BLVD & COUNTY LINE RD - SE CORNER, WESLEY CHAPEL, PASCO COUNTY, FLORIDA 33543
MEADOW POINTE II COMMUNITY DEVELOPMENT DISTRICT
WESLEY CHAPEL, PASCO COUNTY, FLORIDA 33543

**PROJECT NO.:2421.01**
**DATE: 06/24/2026**
**DRAWN BY:YS**
**REVISIONS:**

**SHEET TITLE:**
MAINTENANCE BLDG. REFLECTED CEILING PLANS

**SHEET NO.:**
A7.2

7/2/2026 11:58:15 AM
Autodesk Docs://2421.01 MPII Community Hall & Facilities Maintenance/2421.01 - Meadow Pointe II Community Bldg.rvt

**SCOPE OF WORK: 07/09/2026**

**Meadow Pointe II CDD – Meeting Hall, Maintenance Bldg. & Sitework**
**Address: SE Corner Block of Mansfield Blvd. & County Line Rd.**

**Scope of Work Description:**
The AE Scope Includes: Code Research and Program Development , Limited Surveying & SUE, Code Research, Schematic Design, Design Development, Construction Documents S&S, Bidding Assistance, Permitting Assistance, & CA Services. Civil, MEP, & Structural Engineering.
**(See Updated VE Conceptual Design Package for Details, Dated 07/02/2026)**

**Bldg. 01: Meeting Hall:** Area: 5,450 GSF
**Bldg. 02: Facilities Maintenance Bldg.:** Area: 2,385 GSF
**Sitework:** Area: 1.9 Acres
**Construction Budget: <TBD>**

Architectural
- Project/ Design Team Administration - Code Research/Summary - Architectural Site Plan
- Design Drawings (Plans, Elevations, Sections, Details) - General and Specific Notes - Specifications
- Room Finish Schedules - Door Hardware Schedules - Partition Schedules

Structural Engineering
- Structural Design - Code Research/Engineering Analysis - Notes/ Specifications
- Design Drawings (Plans, Elevations, Details) - General and Specific Notes, Schedules

MEP Engineering
- MEP Design - Code Research/Engineering Analysis - Notes/ Specifications
- Design Drawings (Plans, Elevations, Details) - General and Specific Notes, Schedules

Civil & Surveying
- Limited Surveying and SUE work - Field Verification - Civil Design - Code Research
- Design Drawings (Plans, Sections, Details) - General and Specific Notes, Schedules

Exclusions: Environmental, Geotech

**Tasks:**

**Task 1 – Code Research and Program Development**
The A/E will provide code research and analysis for all parts of the work including Civil, Architectural, Structural, & MEP. We will provide continued program development to include Structural & MEP Engineering into the current Program that was established in the previous Conceptual Design phase.

**Task 2 – Surveying & SUE (Subsurface Utility) Verification**
The A/E will provide limited Surveying and SUE work for the scope of work site areas for topography, hardscape, landscaping, storm drainage, sanitary, water, electrical, telecomm, gas, and any other subsurface utilities that may be affected by the work.

**Task 3 – Schematic Design**
The A/E will produce schematic design drawings, floor plans & elevations, confirming the programmatic goals. MEP & Civil narrative. Specifications shall be identified and outlined by a table of contents. VE changes as need for Owner's budget.

**Task 4 – Design Development**
The A/E will produce design development drawings: Cover sheet, general information & code summary sheet, existing/demolition floor & reflected ceiling plans, proposed floor & reflected ceiling plans, building elevations, sections, details, and specifications. Includes MEP & Civil.

**Task 5 – Construction Documents**
The A/E will produce construction document permit drawings and specifications for construction: Cover sheet, general information & code summary sheet, existing/demolition floor & reflected ceiling plans, proposed floor & reflected ceiling plans, building elevations, sections, details, notes, schedules, construction details, and specifications. Includes MEP & Civil. Signed & sealed construction documents for permitting.

**Task 6 – Bidding Assistance**
The A/E will assist with Bidding: review pre-bid RFI's and providing responses, preparing addenda to the contract documents as necessary, and review of bids.

**Task 7 – Permitting Assistance**
The A/E will assist with Permitting: Prepare digitally signed & sealed contract documents for permitting submittal by the Contractor. Respond to permit review comments and make revisions to the contract documents as needed.

**Task 8 – Construction Administration**
The A/E will provide Construction Administration: Review of submittals and RFI's, issuance of ASI's and PR's, review of applications for payment, construction project site visits with field reports, substantial completion and final completion inspections, and close-out documents review.

**Tentative Delivery Schedule:**

| | |
|---|---|
| Task 1 Code Research and Program Development | 21 Days |
| Task 2 Surveying & SUE | 28 Days |
| Task 3 Schematic Design | 28 Days |
| Task 4 Design Development | 28 Days |
| Task 5 Construction Documents | 28 Days |
| Total | 134 Days |
| Task 6 Bidding Assistance | (TBD) |
| Task 7 Permitting Assistance | (TBD) |
| Task 8 Construction Administration | (TBD) |
| Construction Meetings/ Site Visits (12 Visits) | |
| Substantial Completion & Final Inspection (2 Visits) | |