39/77

PLAT BOOK PAGE NO.

MEADOW POINTE PARCEL 17 UNIT 3

SECTION 33, TOWNSHIP 26 SOUTH, RANGE 20 EAST, PASCO COUNTY, FLORIDA

LEGAL DESCRIPTION AND DEDICATION.

STATE OF FLORIDA)
COUNTY OF PASCO) ss

The undersigned, owners of the lands shown on this plat to be known as MEADOW POINTE PARCEL 17 UNIT 3, a subdivision of a portion of the Northeast 1/4 of Section 33, Township 26 South, Range 20 East, Pasco County, Florida, and being more particularly described as follows

BEGINNING at the Northeast corner of said Northeast 1/4 of Section 33, run thence along the East boundary of said Section 33, S.00°11'36"W., 1899 46 feet to the Northeast corner of MEADOW POINTE PARCEL 18 UNIT 2, according to the plat thereof as recorded in Plat Book 39, Pages 44 through 49, inclusive of the Public Records of Pasco County, Florida, thence along the Northerly boundary of said MEADOW POINTE PARCEL 18 UNIT 2, the following five (5) courses 1) S.78°47'40"W, 839 71 feet, 2) S 03°30'00"E, 120 00 feet, 3) S 86°30'00"W., 160 00 feet, 4) N.03°30'00"W, 217 57 feet, 5) S 86°30'00"W, 583 94 feet to the Northeast corner of MEADOW POINTE PARCEL 18 UNITS 1 AND 3, according to the plat thereof as recorded in Plat Book 37, Pages 95 through 105, inclusive of the Public Records of Pasco County, Florida, thence along the Northerly boundary of said MEADOW POINTE PARCEL 18 UNITS 1 AND 3, S 80°19'29"W, 178 52 feet to the Southeast corner of MEADOW POINTE PARCEL 17 UNIT 1, according to the plat thereof as recorded in Plat Book 37, Pages 28 through 33, inclusive of the Public Records of Pasco County, Florida, thence along the Easterly boundary of said MEADOW POINTE PARCEL 17 UNIT 1, N 35°00'00"E, 830 04 feet to the Southerlymost corner of MEADOW POINTE PARCEL 17 UNIT 2, according to the plat thereof as recorded in Plat Book 37, Pages 81 through 85, inclusive of the Public Records of Pasco County, Florida, thence along the Easterly boundary of said MEADOW POINTE PARCEL 17 UNIT 2, the following seven (7) courses 1) continue, N 35°00'00"E, 120 94 feet, 2) N 22°00'00"E, 331 50 feet to a point on a curve, 3) Easterly, 33 83 feet along the arc of a curve to the left having a radius of 425 00 feet and a central angle of 04°33'39" (chord bearing N 78°48'48"E, 33 82 feet), 4) N 13°28'02"W, 50 00 feet, 5) N 22°00'00"E, 178 16 feet, 6) N 08°54'00"W, 77 69 feet, 7) N 00°02'51"E, 658 00 feet to the Northeast corner of said MEADOW POINTE PARCEL 17 UNIT 2, said point also being a point on the North boundary of the aforesaid Section 33, thence along said North boundary of Section 33, S 89°57'09"E, 1008 15 feet to the POINT OF BEGINNING

Containing 55 380 acres, more or less

Have cause said land to be divided and subdivided as shown hereon, Trout Creek Properties, LLC ("Trout Creek") and Meadow Pointe II Community Development District (the "District"), as respective owners of the lands described above, do hereby dedicate to the perpetual use of the public and Pasco County, Florida (the "County"), all lands upon which or within which utility improvements and facilities exist, and further do hereby dedicate to the perpetual use of the public and the County, all utility improvements and facilities, including but not limited to, water or sewer lines or pipes, fire hydrants, wells, lift stations, pumping stations, buildings, sewage disposal plants, other utility plants and other appurtenant facilities lying within or upon the lands depicted on this plat and shown on the as-built plans filed with the County for such lands, and further do hereby dedicate to the County a perpetual easement over and across the Drainage Easement and Wetland Conservation Easement areas for the purpose of maintaining or operating the drainage facilities situated thereon, and further do hereby grant the County a perpetual easement over and across all street rights-of-way as shown and depicted hereon for any and all governmental purposes used and including (without limitation) fire and police protection, and emergency medical services, and further do hereby reserve unto themselves, their respective heirs, successors, assigns, or legal representatives, the right to construct, operate, and maintain all such utility improvements, or utilities and appurtenances until such time as the operation and maintenance of said lands, improvements, facilities, and appurtenances is assumed by the County, and further do hereby reserve unto themselves, their respective heirs, successors, assigns, or legal representatives the title to any lands or improvements dedicated to the public or to the County, if for any reason such dedication shall be either voluntarily vacated, voided, or invalidated It is the intention of the owner of the lands described above that the District shall construct, operate, and maintain all street right-of-way as shown and depicted hereon, the drainage facilities and any improvements located therein The District shall have the right at all times to enter upon the Drainage Easements and the Wetland Conservation Easements, and all other easement areas depicted hereon to accomplish such purposes

TROUT CREEK PROPERTIES, LLC - OWNER

The developer acknowledges that he has read, understood, and accepted the above listed conditions of approval

Stuart B. Aronoff — Witness, Linda J Papciak — Witness, Geraldine Burton

Stuart B Aronoff, Vice President

ACKNOWLEDGEMENTS

STATE OF FLORIDA)
COUNTY OF HILLSBOROUGH) SS

I hereby certify on this 28 day of June, 2000, A D, before me personally appeared Stuart B Aronoff, to me known to be the person described in and who executed the foregoing document and severally acknowledged the execution thereof to be his free act and deed for the uses and purposes therein expressed

Witness my hand and official seal at Tampa, Florida, the day and year aforesaid

Pamela J Braun
Notary Public, State of Florida at Large
Pamela J Braun

PAMELA J BRAUN
MY COMMISSION # CC 825547
EXPIRES June 7, 2003

MEADOW POINTE II COMMUNITY DEVELOPMENT DISTRICT - OWNER

Donald A Buck, Chairman — Witness, Karen S Birx — Witness, John R Toborg

ACKNOWLEDGEMENTS

STATE OF FLORIDA)
COUNTY OF HILLSBOROUGH) SS

I hereby certify on this 8th day of June, 2000, A D, before me personally appeared Donald A Buck, to me known to be the person described in and who executed the foregoing document and severally acknowledged the execution thereof to be his free act and deed for the uses and purposes therein expressed

Witness my hand and official seal at Tampa, Florida, the day and year aforesaid

Pamela J Braun
Notary Public, State of Florida at Large
Pamela J Braun

PAMELA J BRAUN
MY COMMISSION # CC 825547
EXPIRES June 7 2003

NOTE Tracts "A", "B", "C", "D" "E", and "F" are not dedicated to the public Legal title to said Tracts "A", "B", "C", "D", "E", and "F" as shown and depicted hereon shall be conveyed by Trout Creek to the District, and maintained by said District

JOB NO DDT-TC-535
P \Meadow Pointe\MP17-3-1

CERTIFICATE OF TITLE

STATE OF FLORIDA)
) ss
COUNTY OF PASCO)

I, Marcia E Rendueles, President of Title Experts of Tampa, Inc, do hereby certify that as described and shown on this plat is in the name of the person, persons, corporation or entity executing this dedication, I hereby certify that the developer of the platted subdivision has record title to that land Additionally, I certify that there are no liens and or encumbrances of record against said property, *except as shown on said plat, and that the taxes for the year 1999, have been paid

This 8th day of June, A D, 2000

Title Experts of Tampa, Inc
By Marcia E Rendueles
Marcia E Rendueles, President

CLERK OF THE CIRCUIT COURT

I hereby certify, that the foregoing plat has been filed in the Public Records of Pasco County, Florida this 2 day of SEPTEMBER, 2000 AD in Plat Book 39, Pages 77, 77-79, 80, 81, 82, 83 & 84

Clerk of the Circuit Court

BOARD OF COUNTY COMMISSIONERS

This is to certify, that on SEPTEMBER 6, 2000, the foregoing plat or plan was approved by the Board of County Commissioners of Pasco County, Florida

Chairman of the Board of County Commissioners

REVIEW OF PLAT BY REGISTERED SURVEYOR

Reviewed for compliance with Chapter 177 of the Florida Statues on this the 25th day of August, 2000

Surveyor's Name Nellie Mae Robinson
Florida Professional Surveyor and Mapper No 3392

SURVEYOR'S CERTIFICATE

I hereby certify that this plat was prepared under my direction and supervision and that it complies with all of the survey requirements of Chapter 177 of the Florida Statutes, and that the "P R M 's" (Permanent Reference Monuments) as shown hereon have been set, and that the "P C P 'S" (Permanent Control Points) as shown hereon, and all other monumentation of lot corners, points of intersection and changes of direction of lines within the subdivision as required by said Chapter 177 of the Florida Statutes will be set within the time allotted in 177 091 (8) (9)

HEIDT & ASSOCIATES, INC, (LB148)
2212 Swann Avenue
Tampa, Florida 33606

Arthur W Merritt, (LS4498)
Florida Professional Surveyor and Mapper

June 8, 2000
Date

NOTICE. This plat, as recorded in its graphic form, is the official depiction of the subdivided lands described herein and will in no circumstances be supplanted in authority by any other graphic or digital form of the plat There may be additional restrictions that are not recorded on this plat that may be found in the public records of this county

2212 SWANN AVENUE
TAMPA, FLORIDA 33606
(813) 253-5311
HEIDT & ASSOCIATES, INC.
LICENSED BUSINESS NUMBER LB148
CIVIL ENGINEERING
LAND SURVEYING

39/78

PLAT BOOK PAGE NO

MEADOW POINTE PARCEL 17 UNIT 3

SECTION 33, TOWNSHIP 26 SOUTH, RANGE 20 EAST, PASCO COUNTY, FLORIDA

CABLE TELEVISION NOTE

Utility easements shall provide that such easements shall also be easements for the construction, installation, maintenance, and operation of cable television services, provided, however, no such construction, installation, maintenance, and operation of cable television services shall interfere with the facilities and services of an electric, telephone, gas or other public utility


State Plane Coordinates as shown hereon are in compliance with National Ocean Service standards with geodetic positions rigidly adjusted to the North America Datum of 1983 as readjusted in 1990


N

SCALE 1" = 200'

0 100 200 400

SCALE IN FEET

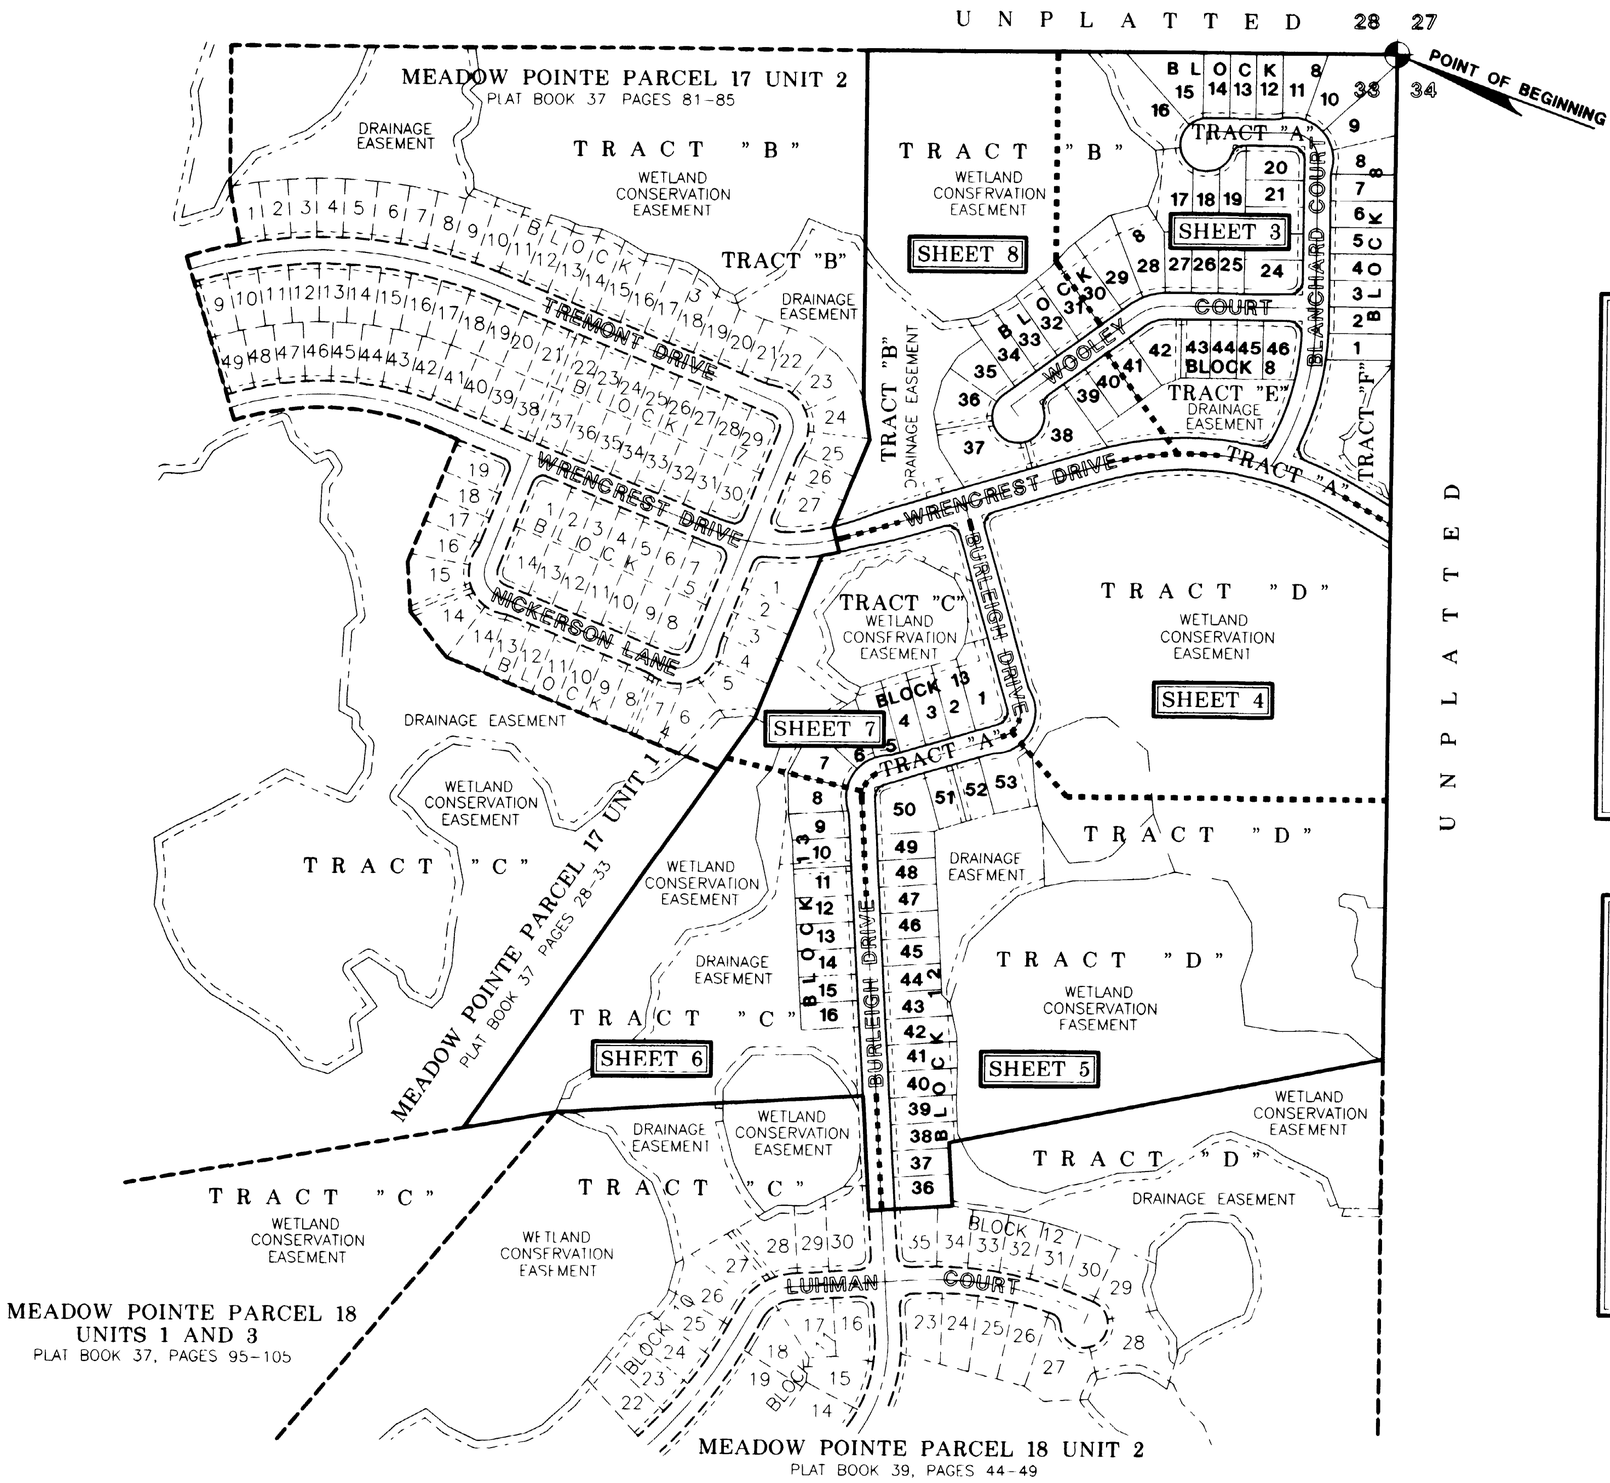

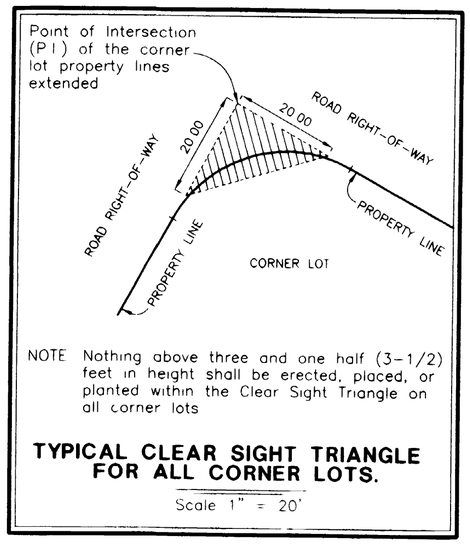


NOTE Nothing above three and one half (3-1/2) feet in height shall be erected, placed, or planted within the Clear Sight Triangle on all corner lots

TYPICAL CLEAR SIGHT TRIANGLE FOR ALL CORNER LOTS.

Scale 1" = 20'

Note In the case where the location of a P C P falls in the top of a Sanitary Manhole or other Utility Structure and it can not be set, four (4) reference points are set establishing two lines that intersect at the P C P location

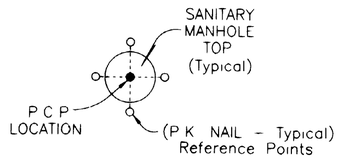

P.C.P. REFERENCE DIAGRAM

(NOT TO SCALE)

KEY SHEET

NOTE REFER TO THE FOLLOWING SHEETS OF THIS PLAT FOR DETAILED LABELLING AND DIMENSIONING

2212 SWANN AVENUE
TAMPA, FLORIDA 33606
(813) 253-5311


HEIDT & ASSOCIATES, INC
LICENSED BUSINESS NUMBER LB148
CIVIL ENGINEERING
LAND SURVEYING

39/79

PLAT BOOK PAGE NO


MEADOW POINTE PARCEL 17 UNIT 3

SECTION 33, TOWNSHIP 26 SOUTH, RANGE 20 EAST, PASCO COUNTY, FLORIDA

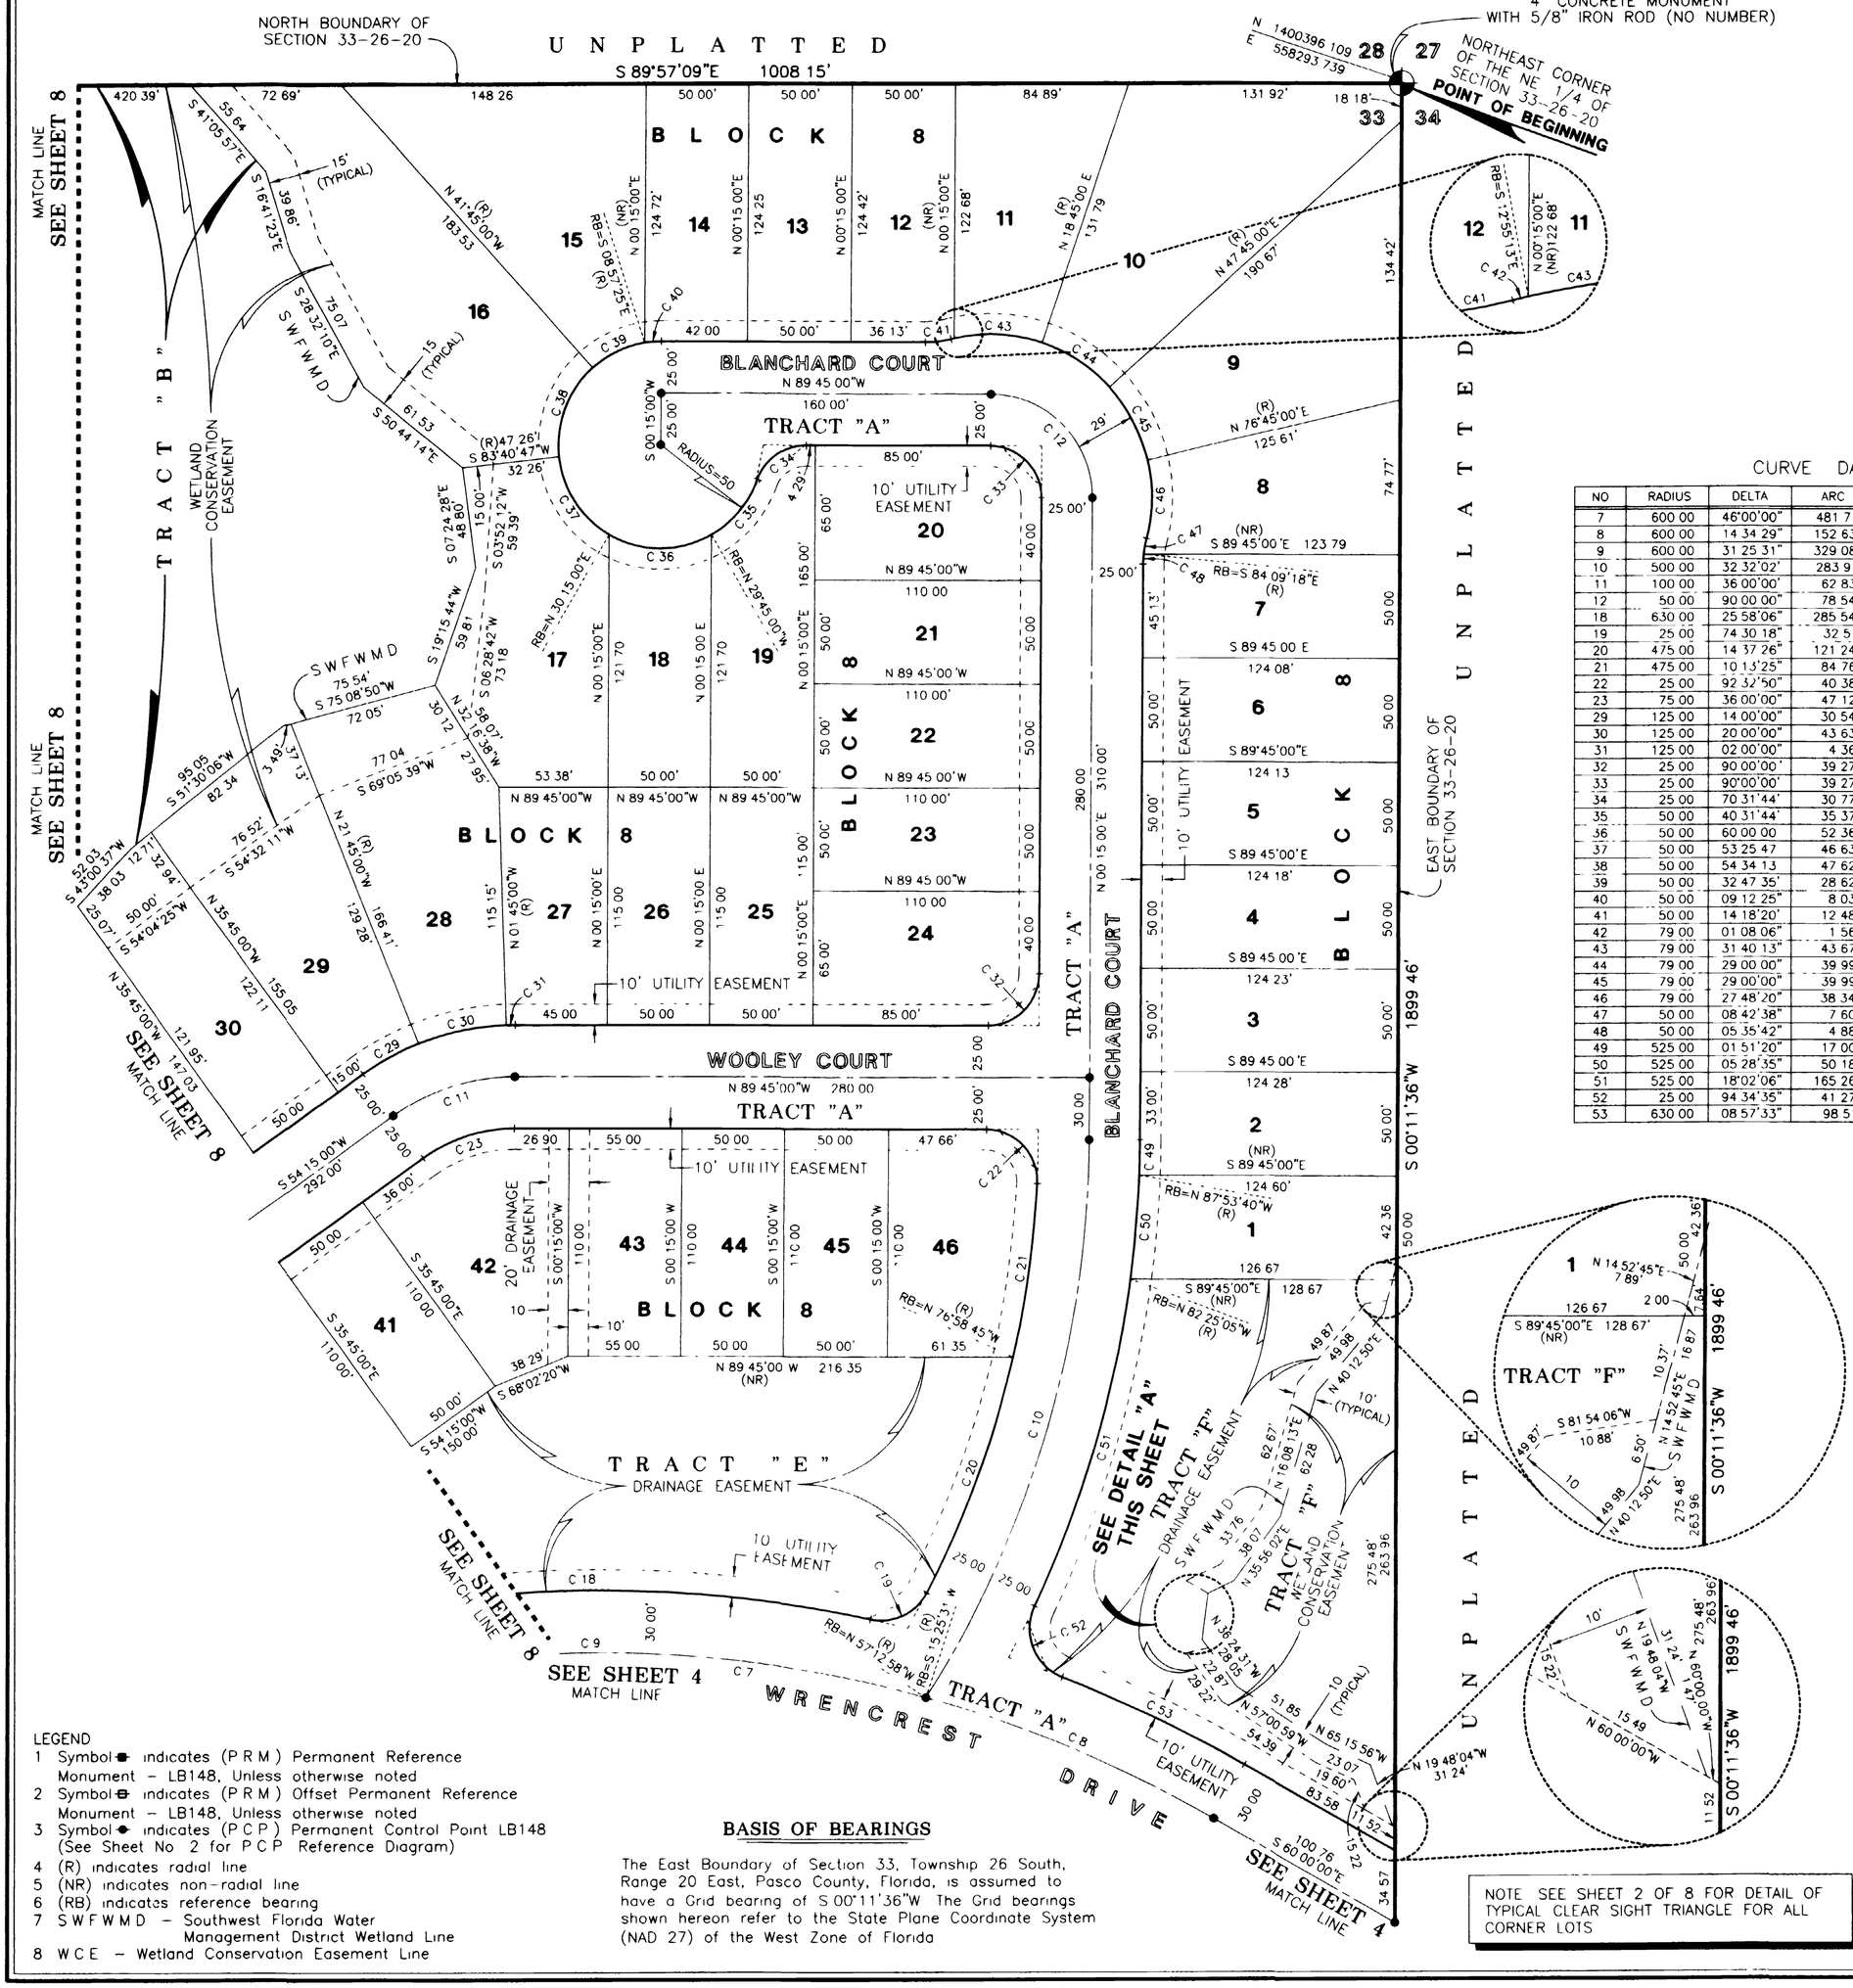

CURVE DATA TABLE

NO	RADIUS	DELTA	ARC	TANGENT	CHORD	BEARING
7	600 00	46°00'00"	481 71	254 68	468 88	S 83°00 00"E
8	600 00	14 34 29"	152 63	76 73	152 22	N 67 17 15"W
9	600 00	31 25 31"	329 08	168 79	324 97	S 89 42'45"W
10	500 00	32 32'02"	283 91	145 90	280 11	N 16 31 01"E
11	100 00	36 00'00"	62 83	32 49	61 80	S 72 15'00"W
12	50 00	90 00 00"	78 54	50 00	70 71	N 44 45 00"W
18	630 00	25 58'06"	285 54	145 26	283 10	N 89 09'56"E
19	25 00	74 30 18"	32 51	19 01	30 27	N 64 53'50"E
20	475 00	14 37 26"	121 24	60 95	120 91	N 20 19'58"E
21	475 00	10 13'25"	84 76	42 49	84 64	N 07 54 33"E
22	25 00	92 32'50"	40 38	26 14	36 13	N 43 28'35"W
23	75 00	36 00'00"	47 12	24 37	46 35	S 72 15 00"W
29	125 00	14 00'00"	30 54	15 35	30 47	N 61°15 00"E
30	125 00	20 00'00"	43 63	22 04	43 41	N 78 15 00"E
31	125 00	02 00'00"	4 36	2 18	4 36	N 89 15 00"E
32	25 00	90 00'00"	39 27	25 00	35 36	N 45 15 00"E
33	25 00	90°00'00"	39 27	25 00	35 36	N 44°45 00"W
34	25 00	70 31'44"	30 77	17 68	28 87	S 54 59'08"W
35	50 00	40 31'44"	35 37	18 46	34 64	S 39°59'08"W
36	50 00	60 00 00	52 36	28 87	50 00	N 89 45'00"W
37	50 00	53 25 47	46 63	25 16	44 96	N 33 02'07"W
38	50 00	54 34 13	47 62	25 79	45 84	N 20 57'53"E
39	50 00	32 47 35'	28 62	14 71	28 23	N 64 38'48"E
40	50 00	09 12 25"	8 03	4 03	8 03	N 85 38'48"E
41	50 00	14 18'20'	12 48	6 27	12 45	N 83 05'50"E
42	79 00	01 08 06"	1 56	0 78	1 56	N 76 30'43"E
43	79 00	31 40 13"	43 67	22 41	43 11	S 87 05'07"E
44	79 00	29 00 00"	39 99	20 43	39 56	S 56 45'00"E
45	79 00	29 00'00"	39 99	20 43	39 56	S 27 45'00"E
46	79 00	27 48'20"	38 34	19 55	37 96	S 00 39'10"W
47	50 00	08 42'38"	7 60	3 81	7 59	S 10°12'01"W
48	50 00	05 35'42"	4 88	2 44	4 88	S 03 02'51"W
49	525 00	01 51'20"	17 00	8 50	17 00	S 01 10'40"W
50	525 00	05 28'35"	50 18	25 11	50 16	S 04 50 38"W
51	525 00	18°02'06"	165 26	83 32	164 57	S 16 35 59"W
52	25 00	94 34'35"	41 27	27 08	36 74	S 21 40 16"E
53	630 00	08 57'33"	98 51	49 36	98 41	S 64 28 47"E

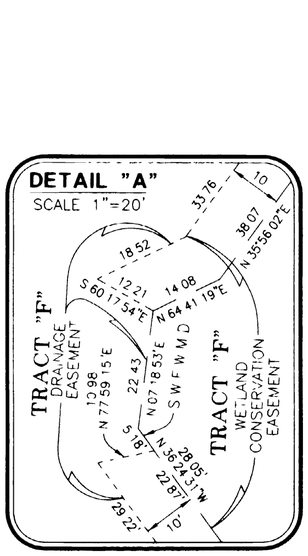

LEGEND

1 Symbol ■ indicates (P R M) Permanent Reference Monument – LB148, Unless otherwise noted
2 Symbol ⊕ indicates (P R M) Offset Permanent Reference Monument – LB148, Unless otherwise noted
3 Symbol ● indicates (P C P) Permanent Control Point LB148 (See Sheet No 2 for P C P Reference Diagram)
4 (R) indicates radial line
5 (NR) indicates non-radial line
6 (RB) indicates reference bearing
7 S W F W M D – Southwest Florida Water Management District Wetland Line
8 W C E – Wetland Conservation Easement Line

BASIS OF BEARINGS

The East Boundary of Section 33, Township 26 South, Range 20 East, Pasco County, Florida, is assumed to have a Grid bearing of S 00°11'36"W The Grid bearings shown hereon refer to the State Plane Coordinate System (NAD 27) of the West Zone of Florida

NOTE SEE SHEET 2 OF 8 FOR DETAIL OF TYPICAL CLEAR SIGHT TRIANGLE FOR ALL CORNER LOTS

2212 SWANN AVENUE
TAMPA FLORIDA 33606
(813) 253-5311


HEIDT & ASSOCIATES, INC
LICENSED BUSINESS NUMBER LB148
CIVIL ENGINEERING
LAND SURVEYING

39/80

PLAT BOOK PAGE NO

MEADOW POINTE PARCEL 17 UNIT 3

SECTION 33, TOWNSHIP 26 SOUTH, RANGE 20 EAST, PASCO COUNTY, FLORIDA

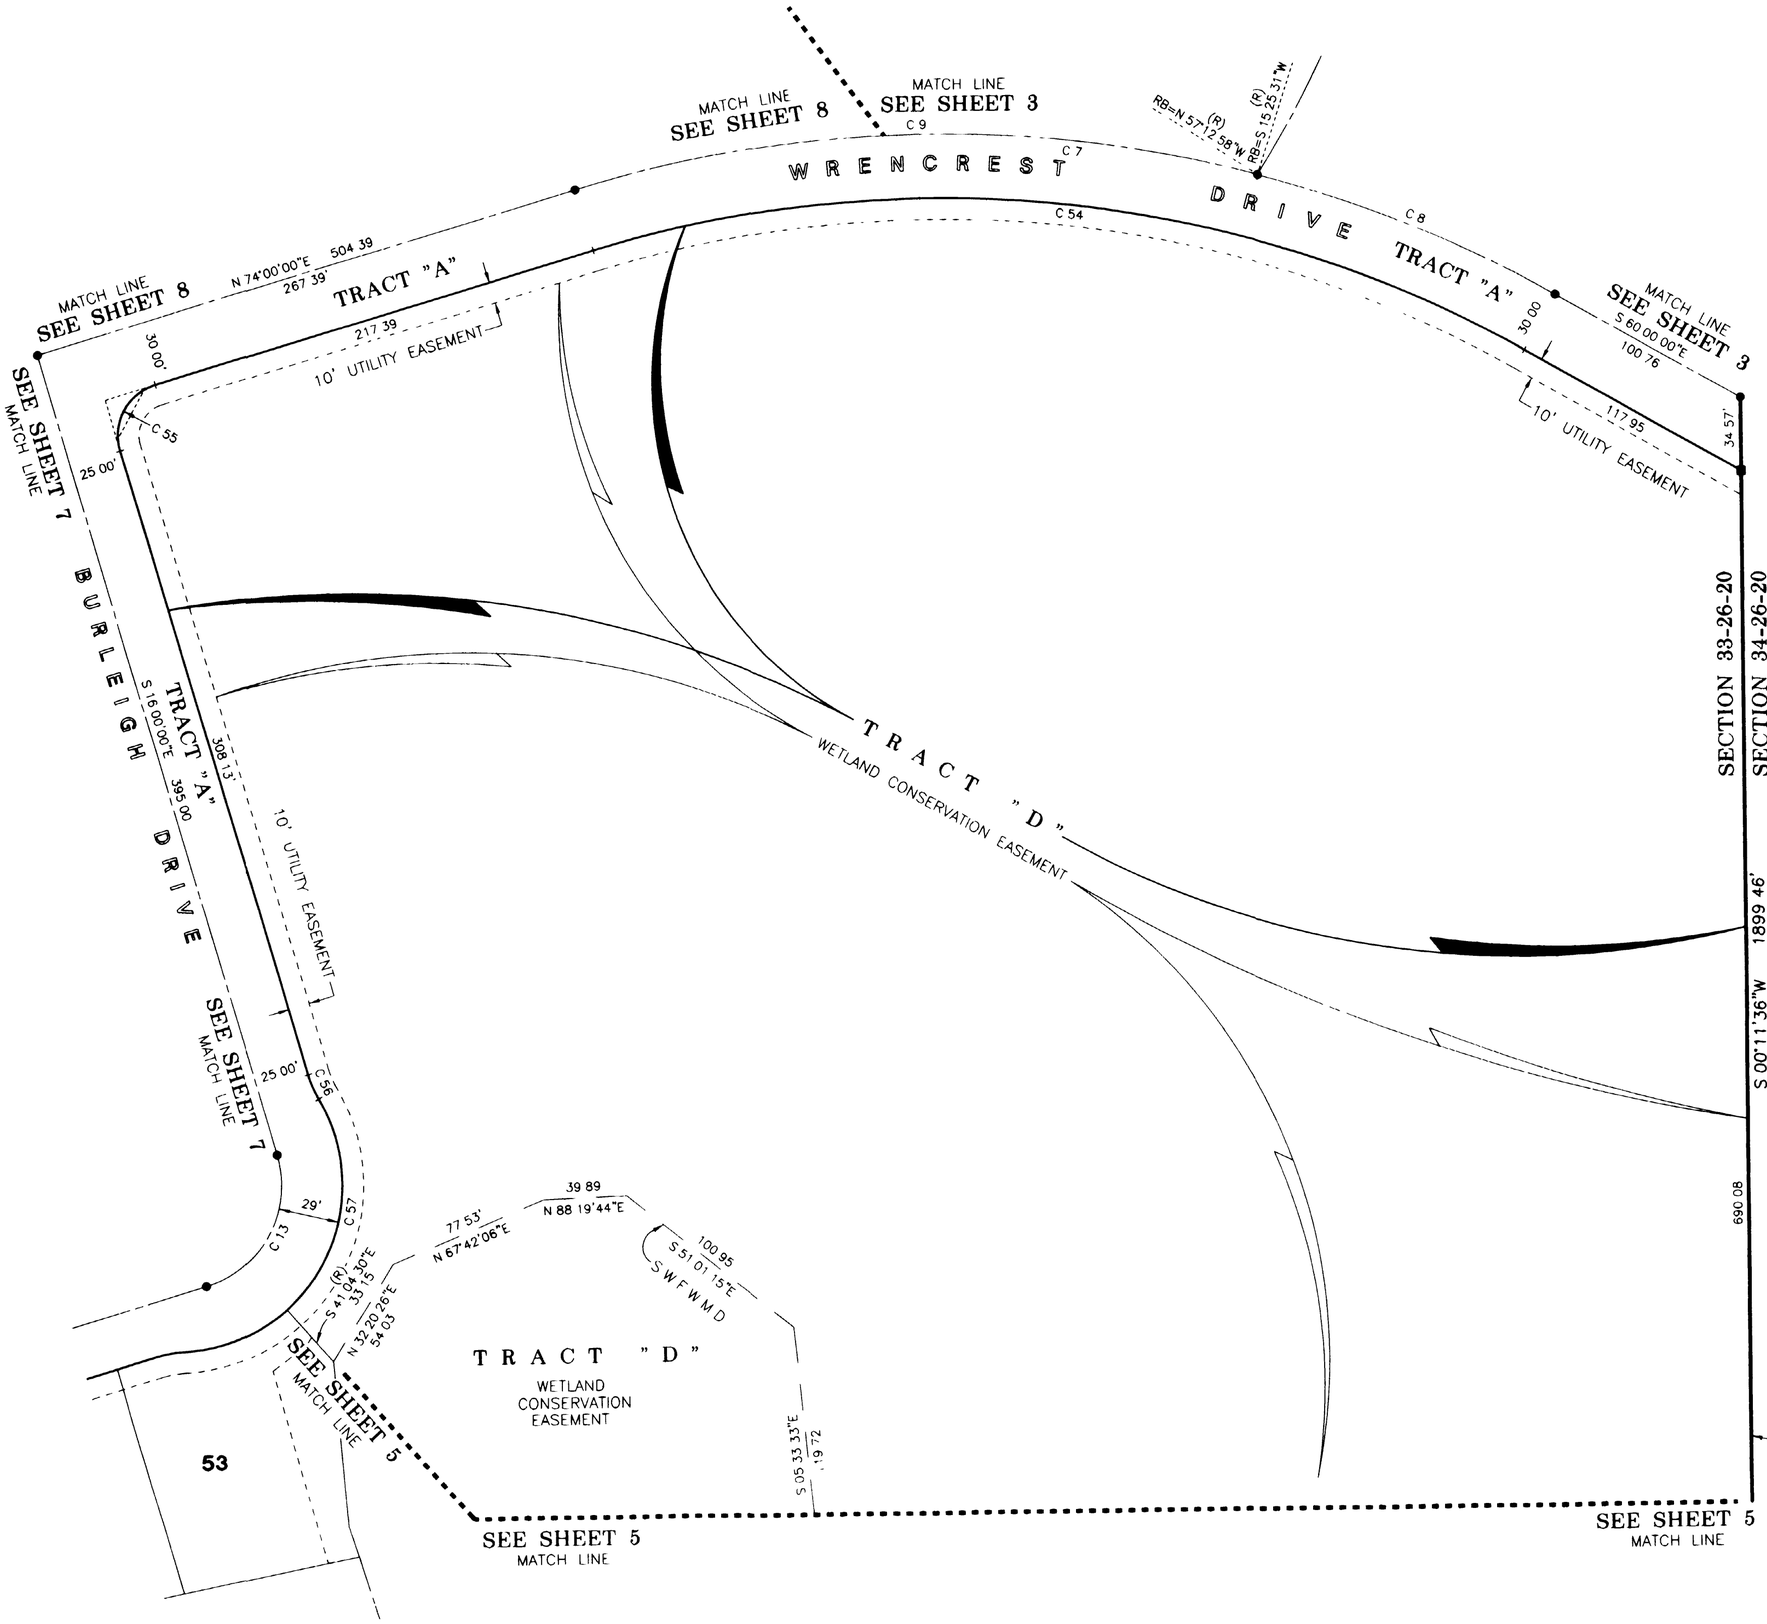

N

SCALE 1" = 50'

0 25 50 100

SCALE IN FEET

SEE NOTE ON SHEET 3 OF 8 FOR BASIS OF BEARINGS

LEGEND

1 Symbol ■ indicates (P R M) Permanent Reference Monument – LB148, Unless otherwise noted
2 Symbol ⊟ indicates (P R M) Offset Permanent Reference Monument – LB148, Unless otherwise noted
3 Symbol ◆ indicates (P C P) Permanent Control Point LB148 (See Sheet No 2 for P C P Reference Diagram)
4 (R) indicates radial line
5 (NR) indicates non-radial line
6 (RB) indicates reference bearing
7 S W F W M D – Southwest Florida Water Management District Wetland Line
8 W C E – Wetland Conservation Easement Line

CURVE DATA TABLE

NO	RADIUS	DELTA	ARC	TANGENT	CHORD	BEARING
7	600 00	46°00'00"	481 71	254 68	468 88	S 83°00'00"E
8	600 00	14 34'29"	152 63	76 73	152 22	N 67 17'15"W
9	600 00	31 25 31'	329 08	168 79	324 97	S 89 42 45"W
13	50 00	90°00'00"	78 54	50 00	70 71	S 29°00'00"W
54	570 00	46 00'00"	457 63	241 95	445 43	N 83 00'00"W
55	25 00	90 00'00"	39 27	25 00	35 36	S 29°00 00"W
56	50 00	14 18 20"	12 48	6 27	12 45	S 23°09 10"E
57	79 00	79°13'50"	109 24	65 39	100 75	S 09°18'35"W

NOTE SEE SHEET 2 OF 8 FOR DETAIL OF TYPICAL CLEAR SIGHT TRIANGLE FOR ALL CORNER LOTS

2212 SWANN AVENUE
TAMPA, FLORIDA 33606
(813) 253-5311
HEIDT & ASSOCIATES, INC
LICENSED BUSINESS NUMBER LB148
CIVIL ENGINEERING
LAND SURVEYING

39/81

PLAT BOOK PAGE NO

MEADOW POINTE PARCEL 17 UNIT 3

SECTION 33, TOWNSHIP 26 SOUTH, RANGE 20 EAST, PASCO COUNTY, FLORIDA

CURVE DATA TABLE

NO	RADIUS	DELTA	ARC	TANGENT	CHORD	BEARING
13	50 00	90 00'00"	78 54	50 00	70 71	S 29 00'00"W
14	50 00	77 30'00"	67 63	40 13	62 59	S 35 15'00"W
58	79 00	39 22 49"	54 30	28 27	53 24	S 68 36 55"W
59	50 00	14 18'20"	12 48	6 27	12 45	S 81 09'10"W
60	25 00	77'30 00'	33 82	20 06	31 30	S 35 15 00"W

N

SCALE 1" = 50'

0 25 50 100

SCALE IN FEET

SEE NOTE ON SHEET 3 OF 8 FOR BASIS OF BEARINGS

NOTE SEE SHEET 2 OF 8 FOR DETAIL OF TYPICAL CLEAR SIGHT TRIANGLE FOR ALL CORNER LOTS

LEGEND

1 Symbol ■ indicates (P R M) Permanent Reference Monument – LB148, Unless otherwise noted
2 Symbol ⊟ indicates (P R M) Offset Permanent Reference Monument – LB148, Unless otherwise noted
3 Symbol ● indicates (P C P) Permanent Control Point LB148 (See Sheet No 2 for P C P Reference Diagram)
4 (R) indicates radial line
5 (NR) indicates non–radial line
6 (RB) indicates reference bearing
7 S W F W M D – Southwest Florida Water Management District Wetland Line

2212 SWANN AVENUE
TAMPA FLORIDA 33606
(813) 253–5311

HEIDT & ASSOCIATES, INC
LICENSED BUSINESS NUMBER LB148
CIVIL ENGINEERING
LAND SURVEYING

39/82

PLAT BOOK PAGE NO

MEADOW POINTE PARCEL 17 UNIT 3

SECTION 33, TOWNSHIP 26 SOUTH, RANGE 20 EAST, PASCO COUNTY, FLORIDA

CURVE DATA TABLE

NO	RADIUS	DELTA	ARC	TANGENT	CHORD	BEARING
14	50 00	77°30'00"	67 63	40 13	62 59	S 35 15'00"W
61	50 00	11 49'31"	10 32	5 18	10 30	N 09 24'46"W
62	50 00	02°28 48"	2 16	1 08	2 16	N 16 33'55"W
63	79 00	30 48'20"	42 47	21 76	41 97	N 02 24'10"W

LEGEND
1 Symbol ■ indicates (P R M) Permanent Reference Monument – LB148, Unless otherwise noted
2 Symbol ⊟ indicates (P R M) Offset Permanent Reference Monument – LB148, Unless otherwise noted
3 Symbol ◆ indicates (P C P) Permanent Control Point LB148 (See Sheet No 2 for P C P Reference Diagram)
4 (R) indicates radial line
5 (NR) indicates non-radial line
6 (RB) indicates reference bearing
7 S W F W M D – Southwest Florida Water Management District Wetland Line

NOTE SEE SHEET 2 OF 8 FOR DETAIL OF TYPICAL CLEAR SIGHT TRIANGLE FOR ALL CORNER LOTS

SCALE 1" = 50'
0 25 50 100
SCALE IN FEET

SEE NOTE ON SHEET 2 OF 8 FOR BASIS OF BEARINGS

MEADOW POINTE PARCEL 17 UNIT 2
PLAT BOOK 37, PAGES 81–85

BLOCK 6

N 35°00'00"E 120 94'

MATCH LINE SEE SHEET 7

EASTERLY BOUNDARY OF MEADOW POINTE PARCEL 17 UNIT 2

SOUTHERLYMOST CORNER OF MEADOW POINTE PARCEL 17 UNIT 2

MEADOW POINTE PARCEL 17 UNIT 1
PLAT BOOK 37, PAGES 28–33

TRACT "C" WETLAND CONSERVATION EASEMENT

N 35°00'00"E 830 04'

EASTERLY BOUNDARY OF MEADOW POINTE PARCEL 17 UNIT 1

SOUTHEAST CORNER OF MEADOW POINTE PARCEL 17 UNIT 1

TRACT "C" DRAINAGE EASEMENT

TRACT "C" WETLAND CONSERVATION EASEMENT

BLOCK 13

8 9 10 11 12 13 14 15 16

20' DRAINAGE EASEMENT

10' UTILITY EASEMENT

TRACT "A"

BURLEIGH DRIVE

SEE SHEET 5 MATCH LINE

TRACT "C" DRAINAGE EASEMENT

TRACT "C" WETLAND CONSERVATION EASEMENT

S 80°19'29"W 178 52'

NORTHERLY BOUNDARY OF MEADOW POINTE PARCEL 18 UNITS 1 AND 3

NORTHEAST CORNER OF MEADOW POINTE PARCEL 18 UNITS 1 AND 3

S 86°30'00"W 583 94'

NORTHERLY BOUNDARY OF MEADOW POINTE PARCEL 18 UNIT 2

MEADOW POINTE PARCEL 18 UNITS 1 AND 3
PLAT BOOK 37, PAGES 95–105

MEADOW POINTE PARCEL 18 UNIT 2
PLAT BOOK 39, PAGES 44–49

BLOCK 10 28 29 30

S 86°30'00"W 160 00'

N 03°30'00"W 217 57'

SEE SHEET 5 MATCH LINE


2212 SWANN AVENUE
TAMPA FLORIDA 33606
(813) 253-5311
HEIDT & ASSOCIATES, INC
LICENSED BUSINESS NUMBER LB148
CIVIL ENGINEERING
LAND SURVEYING

39/83

PLAT BOOK PAGE NO

MEADOW POINTE PARCEL 17 UNIT 3

SECTION 33, TOWNSHIP 26 SOUTH, RANGE 20 EAST, PASCO COUNTY, FLORIDA

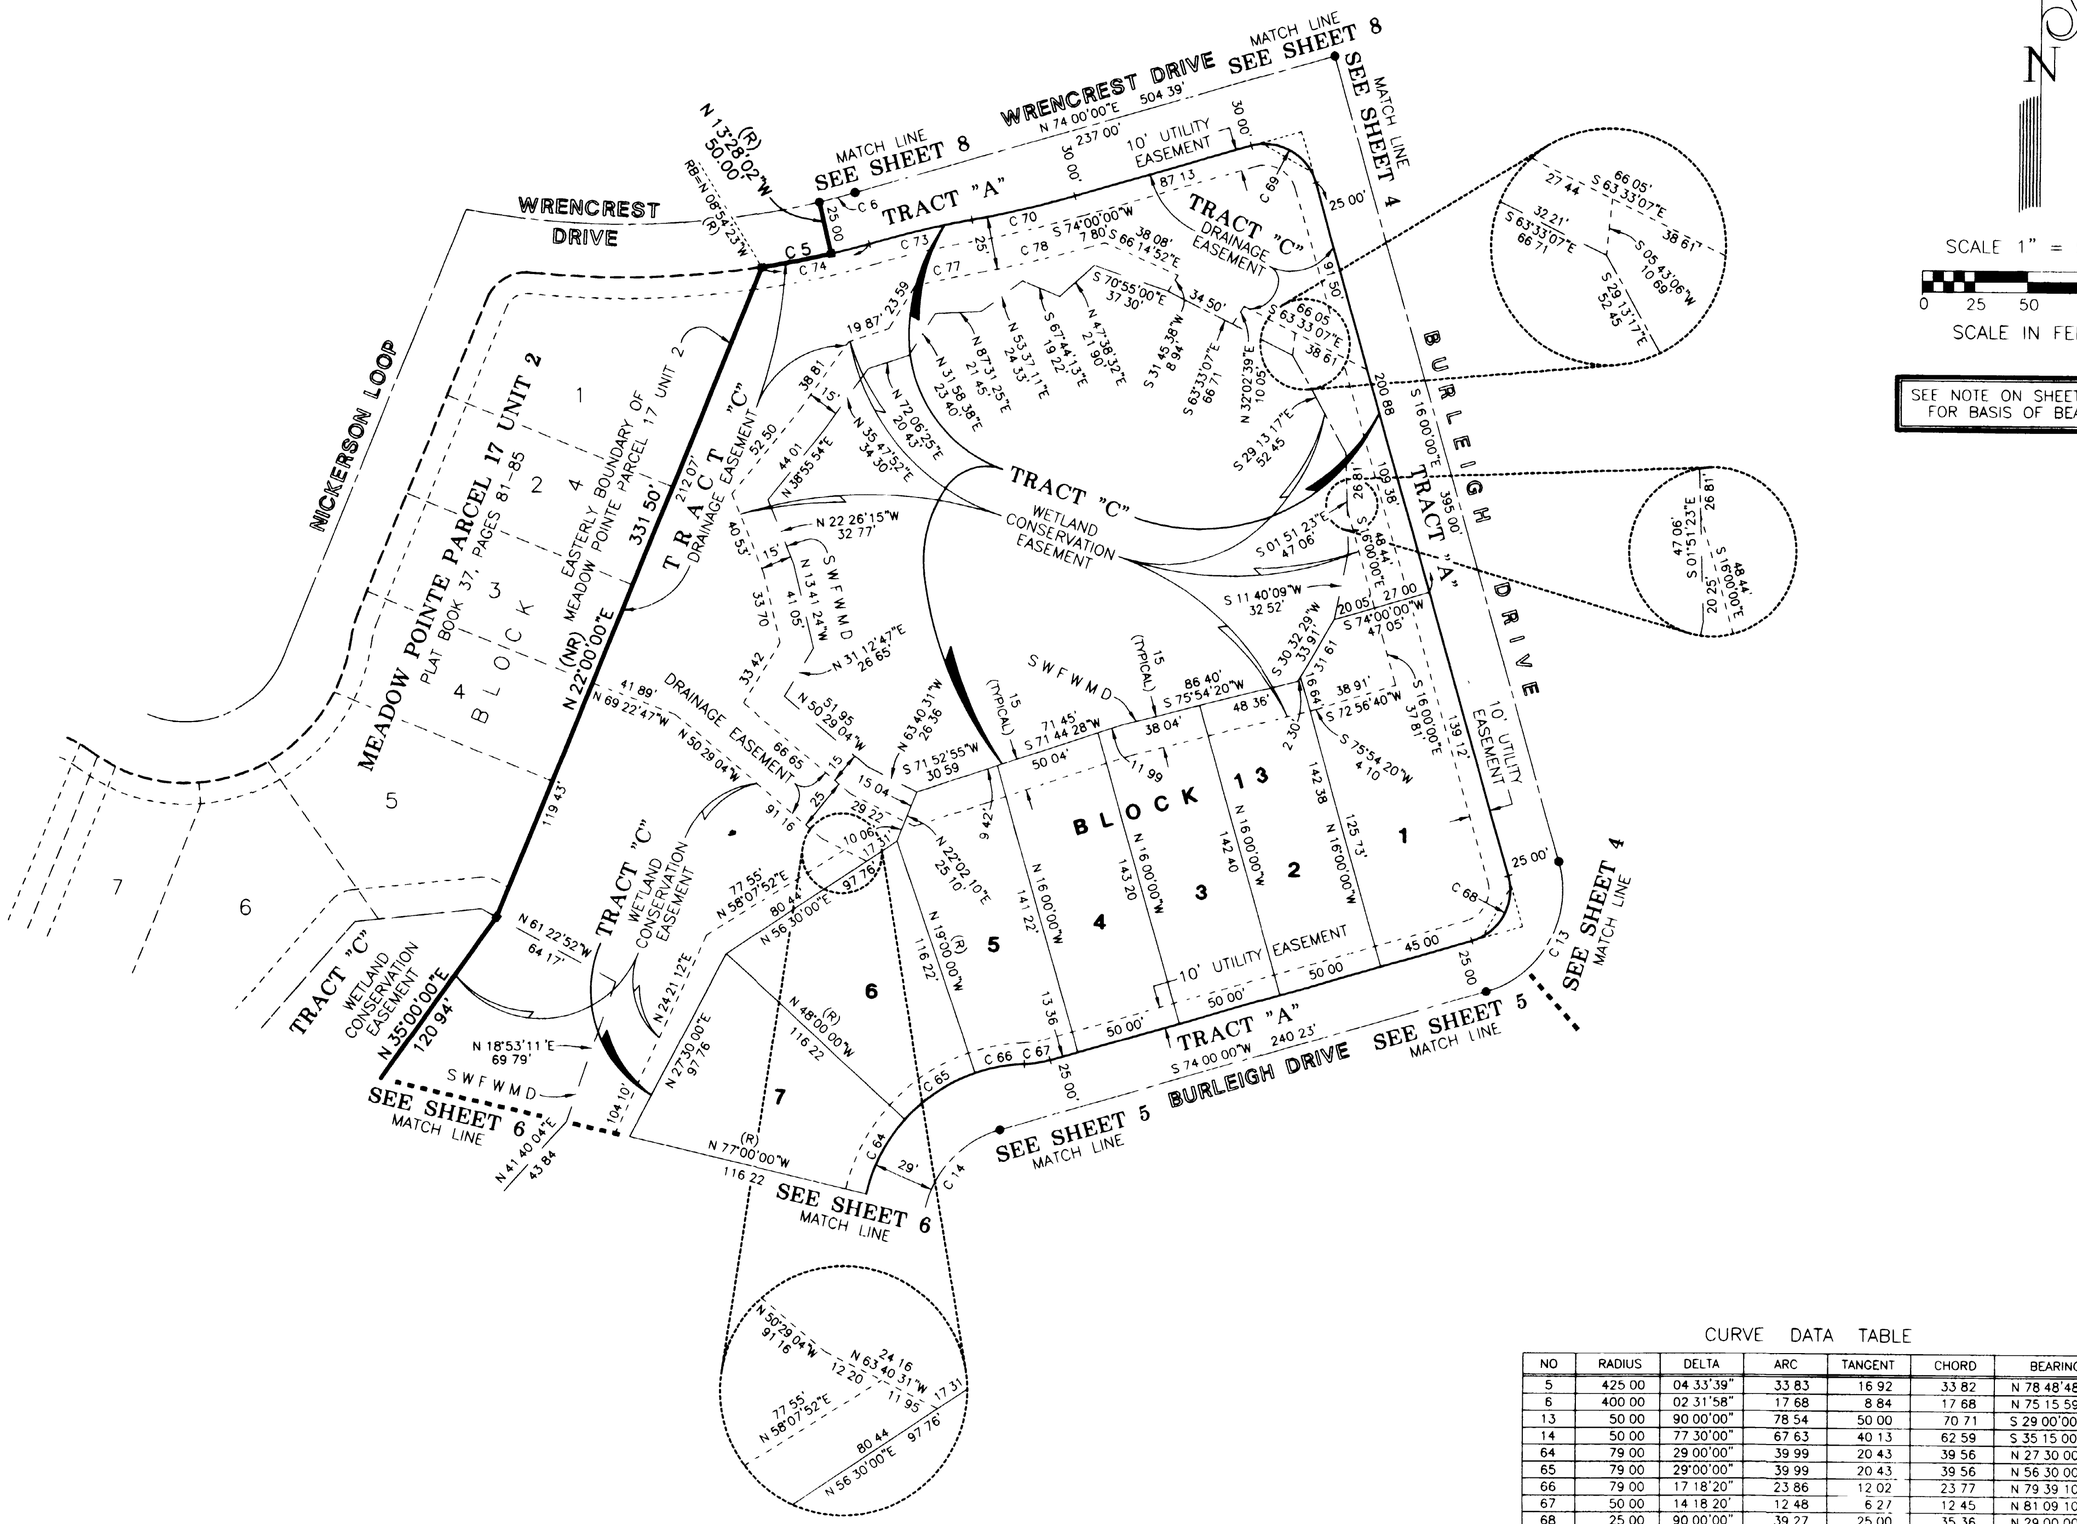

CURVE DATA TABLE

NO	RADIUS	DELTA	ARC	TANGENT	CHORD	BEARING
5	425 00	04 33'39"	33 83	16 92	33 82	N 78 48'48"E
6	400 00	02 31'58"	17 68	8 84	17 68	N 75 15 59 'E
13	50 00	90 00'00"	78 54	50 00	70 71	S 29 00'00"W
14	50 00	77 30'00"	67 63	40 13	62 59	S 35 15 00 W
64	79 00	29 00'00"	39 99	20 43	39 56	N 27 30 00"E
65	79 00	29'00'00"	39 99	20 43	39 56	N 56 30 00"E
66	79 00	17 18'20"	23 86	12 02	23 77	N 79 39 10 E
67	50 00	14 18 20'	12 48	6 27	12 45	N 81 09 10 E
68	25 00	90 00'00"	39 27	25 00	35 36	N 29 00 00 E
69	25 00	90 00 00'	39 27	25 00	35 36	N 61 00 00 W
70	500 00	05'43 55	50 02	25 03	50 00	S 76'51 58 'W
73	500 00	05 43'55"	50 02	25 03	50 00	S 76 51'58"W
74	425 00	07'05 37"	52 62	26 34	52 58	S 77 32'49"W
77	475 00	03'50'57"	31 91	15 96	31 91	N 77'48'26"E
78	525 00	05'43'55"	52 52	26 28	52 50	N 76 51'58"E

LEGEND

1 Symbol ● indicates (P R M) Permanent Reference Monument - LB148, Unless otherwise noted
2 Symbol ⊕ indicates (P R M) Offset Permanent Reference Monument - LB148, Unless otherwise noted
3 Symbol ◆ indicates (P C P) Permanent Control Point LB148 (See Sheet No 2 for P C P Reference Diagram)
4 (R) indicates radial line
5 (NR) indicates non-radial line
6 (RB) indicates reference bearing
7 S W F W M D - Southwest Florida Water Management District Wetland Line
8 W C E - Wetland Conservation Easement Line

NOTE SEE SHEET 2 OF 8 FOR DETAIL OF TYPICAL CLEAR SIGHT TRIANGLE FOR ALL CORNER LOTS

2212 SWANN AVENUE
TAMPA, FLORIDA 33606
(813) 253-5311
HEIDT & ASSOCIATES, INC
LICENSED BUSINESS NUMBER LB148
CIVIL ENGINEERING
LAND SURVEYING

PLAT BOOK PAGE NO.

MEADOW POINTE PARCEL 17 UNIT 3

SECTION 33, TOWNSHIP 26 SOUTH, RANGE 20 EAST, PASCO COUNTY, FLORIDA

CURVE DATA TABLE

NO	RADIUS	DELTA	ARC	TANGENT	CHORD	BEARING
6	400 00	02 31'58"	17 68	8 84	17 68	N 75 15'59"E
7	600 00	46 00'00"	481 71	254 68	468 88	S 83 00'00"E
9	600 00	31 25'31"	329 08	168 79	324 97	S 89 42 45"W
16	500 00	05 43'55"	50 02	25 03	50 00	N 71 08 02"E
17	630 00	02 10'54"	23 99	12 00	23 99	N 75 05 27"E
18	630 00	25 58'06"	285 54	145 26	283 10	N 89 09 56"E
24	25 00	70 31'44"	30 77	17 68	28 87	S 18 59'08"W
25	50 00	90 16'44"	78 78	50 24	70 88	S 28 51 38"W
26	50 00	96 15 00"	83 99	55 77	74 46	N 57'52'30"W
27	50 00	44 00 00"	38 40	20 20	37 46	N 12 15'00"E
28	50 00	20'00 00"	17 45	8 82	17 36	N 44 15'00"E
80	375 00	02'31 58"	16 58	8 29	16 58	N 75 15'59"E
81	500 00	05 43'55"	50 02	25 03	50 00	N 71 08'02"E

LEGEND
1 Symbol ■ indicates (P R M) Permanent Reference Monument – LB148, Unless otherwise noted
2 Symbol ■ indicates (P R M) Offset Permanent Reference Monument – LB148, Unless otherwise noted
3 Symbol ◆ indicates (P C P) Permanent Control Point LB148 (See Sheet No 2 for P C P Reference Diagram)
4 (R) indicates radial line
5 (NR) indicates non–radial line
6 (RB) indicates reference bearing
7 S W F W M D – Southwest Florida Water Management District Wetland Line
8 W C E – Wetland Conservation Easement Line

UNPLATTED
SECTION 28-26-20
SECTION 33-26-20

NORTHEAST CORNER OF MEADOW POINTE PARCEL 17 UNIT 2

NORTH BOUNDARY OF SECTION 33–26–20

S.89°57'09"E. 1008 15'
420 39'

SEE SHEET 3 MATCH LINE

MEADOW POINTE PARCEL 17 UNIT 2
PLAT BOOK 37, PAGES 81–85

TRACT "B"
WETLAND CONSERVATION EASEMENT

EASTERLY BOUNDARY OF MEADOW POINTE PARCEL 17 UNIT 2

366 88'

N 00°02'51"E 658 00'

TRACT "B"
DRAINAGE EASEMENT

N 33°08'42"W 32 83'
N 42°34'26"W 59 14'
15' (TYPICAL)
N 50°45'56"W 116 73'
S 82°09'22"W 69 28'
49 19'
20 09'
32 52'
68 25'
S 61°43'31"W 35 73'
14 59'
S 51°15'45"W 50 07'
15 02'
20 40'
S 61°35'33"W 29 96'
S 51°15'45"W 20 32'
N 35°45'00"W 124 77'
139 79'
N 35°45'00"W 143 68'
N 35°45'00"W 157 32'
110 00'
N 54°15'00"E 55 21'
47 32'
N 34°15'00"E 56 42'
28 21'
N 14°15'00"E 62 22'
N 09°45'00"W 68 02'
34 01'
N 33°45'00"W 57 61'
88 11'
N 74°00'00"E 64 22'
34 22'
30 00'
30 00'
N 16°00'00"W 30 00'
43 82'
N 74°00'00"E 501 68'
264 68'
S 43°00'37"W 52 03'
14 825 07'
100 98'
36 32'
50 00'
S 54°18'29"W
N 35°45'00"W 147 03'
121 95'
N 35°45'00"W 122 00'
142 40'
50 00'
25 00'
S 54°15'00"W 292 00'
50 00'
10' UTILITY EASEMENT
S 35°45'00"E 110 00'
N 35°45'00"W (NR) 146 13'
RB=S 13°49'06"E (R)
35 13'
C 18
C 17
C 9
C 7
C 24
C 25
C 26
C 27
C 28
35 29'
27 00'
RADIUS=50
(R) S 80°15'00"W 110 00'
(R) S 16°00'00"E 51 26'
125 16'
135 58'
69 95'
143 77'
237 00'
30 00'
C 80
C 81
C 16
C 6
25 00'
N 08°54'00"W 77 69'
N 22°00'00"E (NR) 178 16'
29° 12'
RB=N 13°28'02"W (R)
(R) N 13°28'02"W 50 00'

BLOCK 3: 22, 23, 24, 25, 26, 27
BLOCK 8: 31, 32, 33, 34, 35, 36, 37, 38, 39, 40

TREMONT DRIVE
WRENCREST DRIVE
BURLEIGH DRIVE
WOOLEY COURT
TRACT "A"
TRACT "E" DRAINAGE EASEMENT
SEWAGE PUMPING STATION UTILITY EASEMENT
20' DRAINAGE EASEMENT
10' UTILITY EASEMENT
20' UTILITY EASEMENT

SEE SHEET 7 MATCH LINE
SEE SHEET 4 MATCH LINE
SEE SHEET 3 MATCH LINE

SCALE 1" = 50'
0 25 50 100
SCALE IN FEET

SEE NOTE ON SHEET 3 OF 8 FOR BASIS OF BEARINGS

NOTE SEE SHEET 2 OF 8 FOR DETAIL OF TYPICAL CLEAR SIGHT TRIANGLE FOR ALL CORNER LOTS

2212 SWANN AVENUE
TAMPA, FLORIDA 33606
(813) 253-5311
HEIDT & ASSOCIATES, INC
LICENSED BUSINESS NUMBER LB148
CIVIL ENGINEERING
LAND SURVEYING