
MEADOW POINTE
PARCEL 2 UNIT 1

SECTION 31, TOWNSHIP 26 SOUTH, RANGE 20 EAST,
PASCO COUNTY, FLORIDA

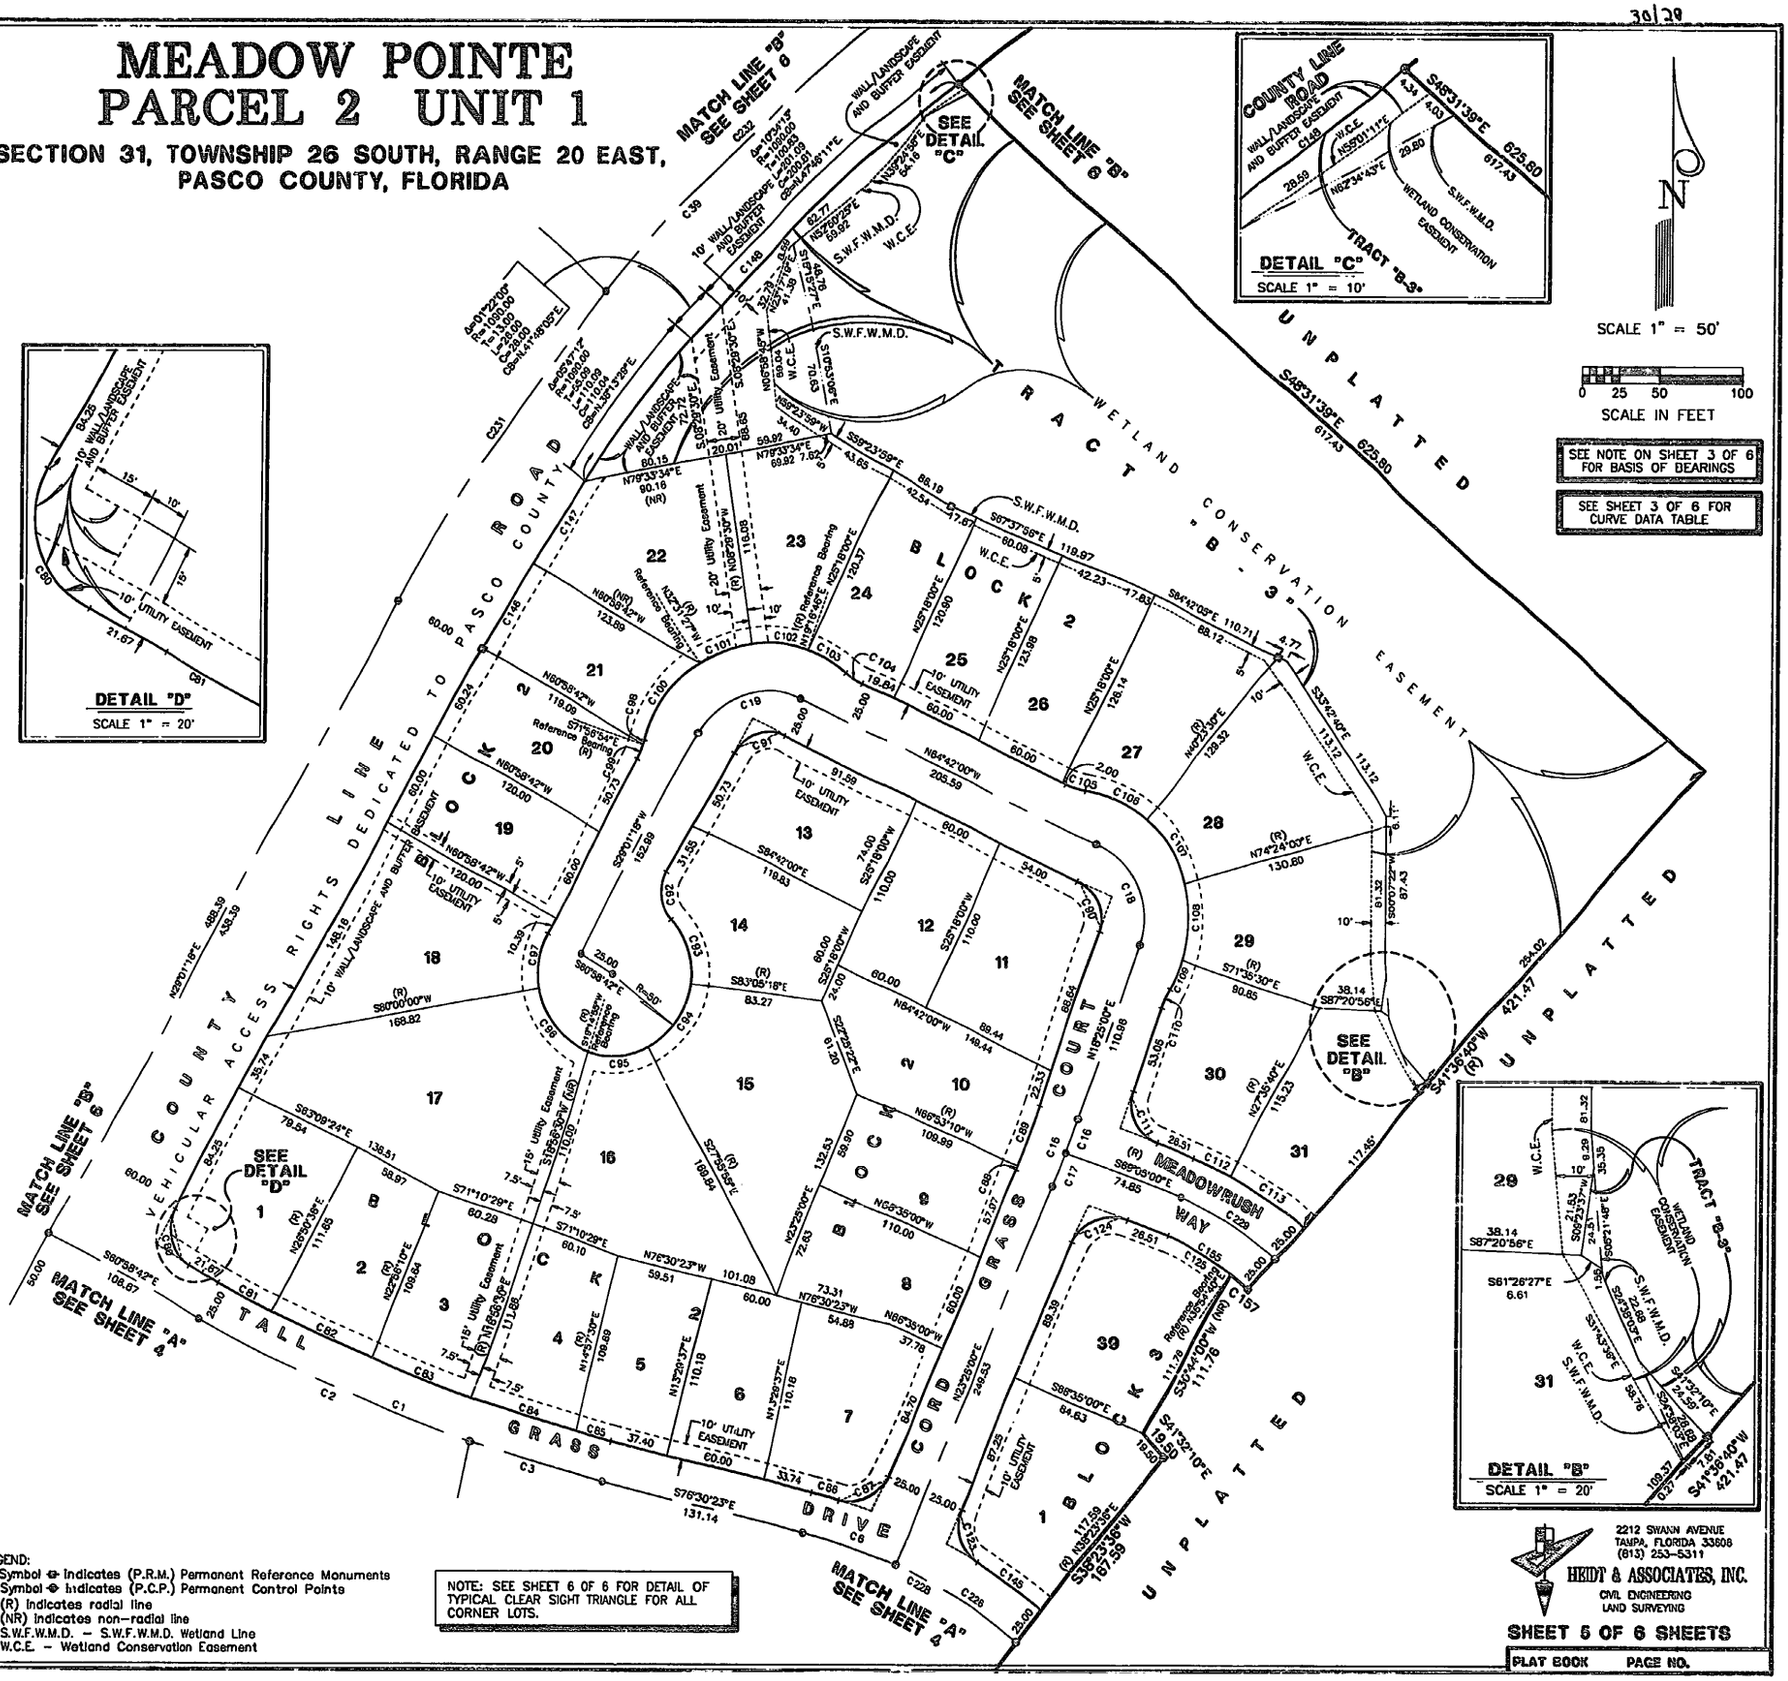

LEGEND:
1. Symbol ⊕ indicates (P.R.M.) Permanent Reference Monuments
2. Symbol ⊕ indicates (P.C.P.) Permanent Control Points
3. (R) indicates radial line
4. (NR) indicates non-radial line
5. S.W.F.W.M.D. – S.W.F.W.M.D. Wetland Line
6. W.C.E. – Wetland Conservation Easement

NOTE: SEE SHEET 6 OF 6 FOR DETAIL OF TYPICAL CLEAR SIGHT TRIANGLE FOR ALL CORNER LOTS.

2212 SWANN AVENUE
TAMPA, FLORIDA 33606
(813) 253-5311
HEIDT & ASSOCIATES, INC.
CIVIL ENGINEERING
LAND SURVEYING

SHEET 5 OF 6 SHEETS

PLAT BOOK PAGE NO.