

MEADOW POINTE PARCEL 2 UNIT 1

SECTION 31, TOWNSHIP 26 SOUTH, RANGE 20 EAST, PASCO COUNTY, FLORIDA

RANGE 19 EAST
RANGE 20 EAST

COUNTY ROAD NO. 581
Order of Taking CASE NO. 2135, March 11, 1968
(200' R/W)

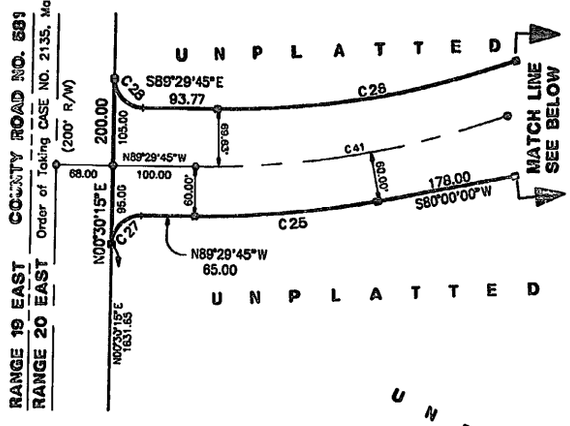


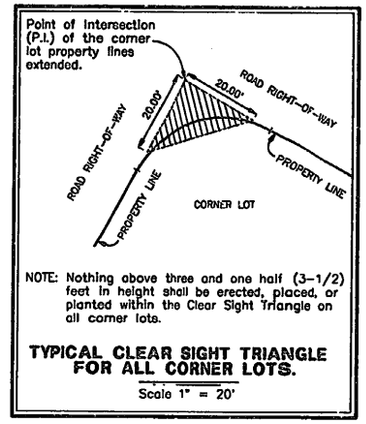

NOTE: Nothing above three and one half (3-1/2) feet in height shall be erected, placed, or planted within the Clear Sight Triangle on all corner lots.

TYPICAL CLEAR SIGHT TRIANGLE FOR ALL CORNER LOTS.

Scale 1" = 20'

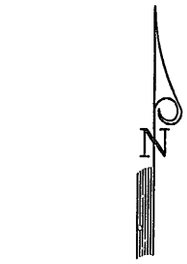


SCALE 1" = 100'

0 50 100 200

SCALE IN FEET

SEE NOTE ON SHEET 3 OF 6 FOR BASIS OF BEARINGS

SEE SHEET 3 OF 6 FOR CURVE DATA TABLE

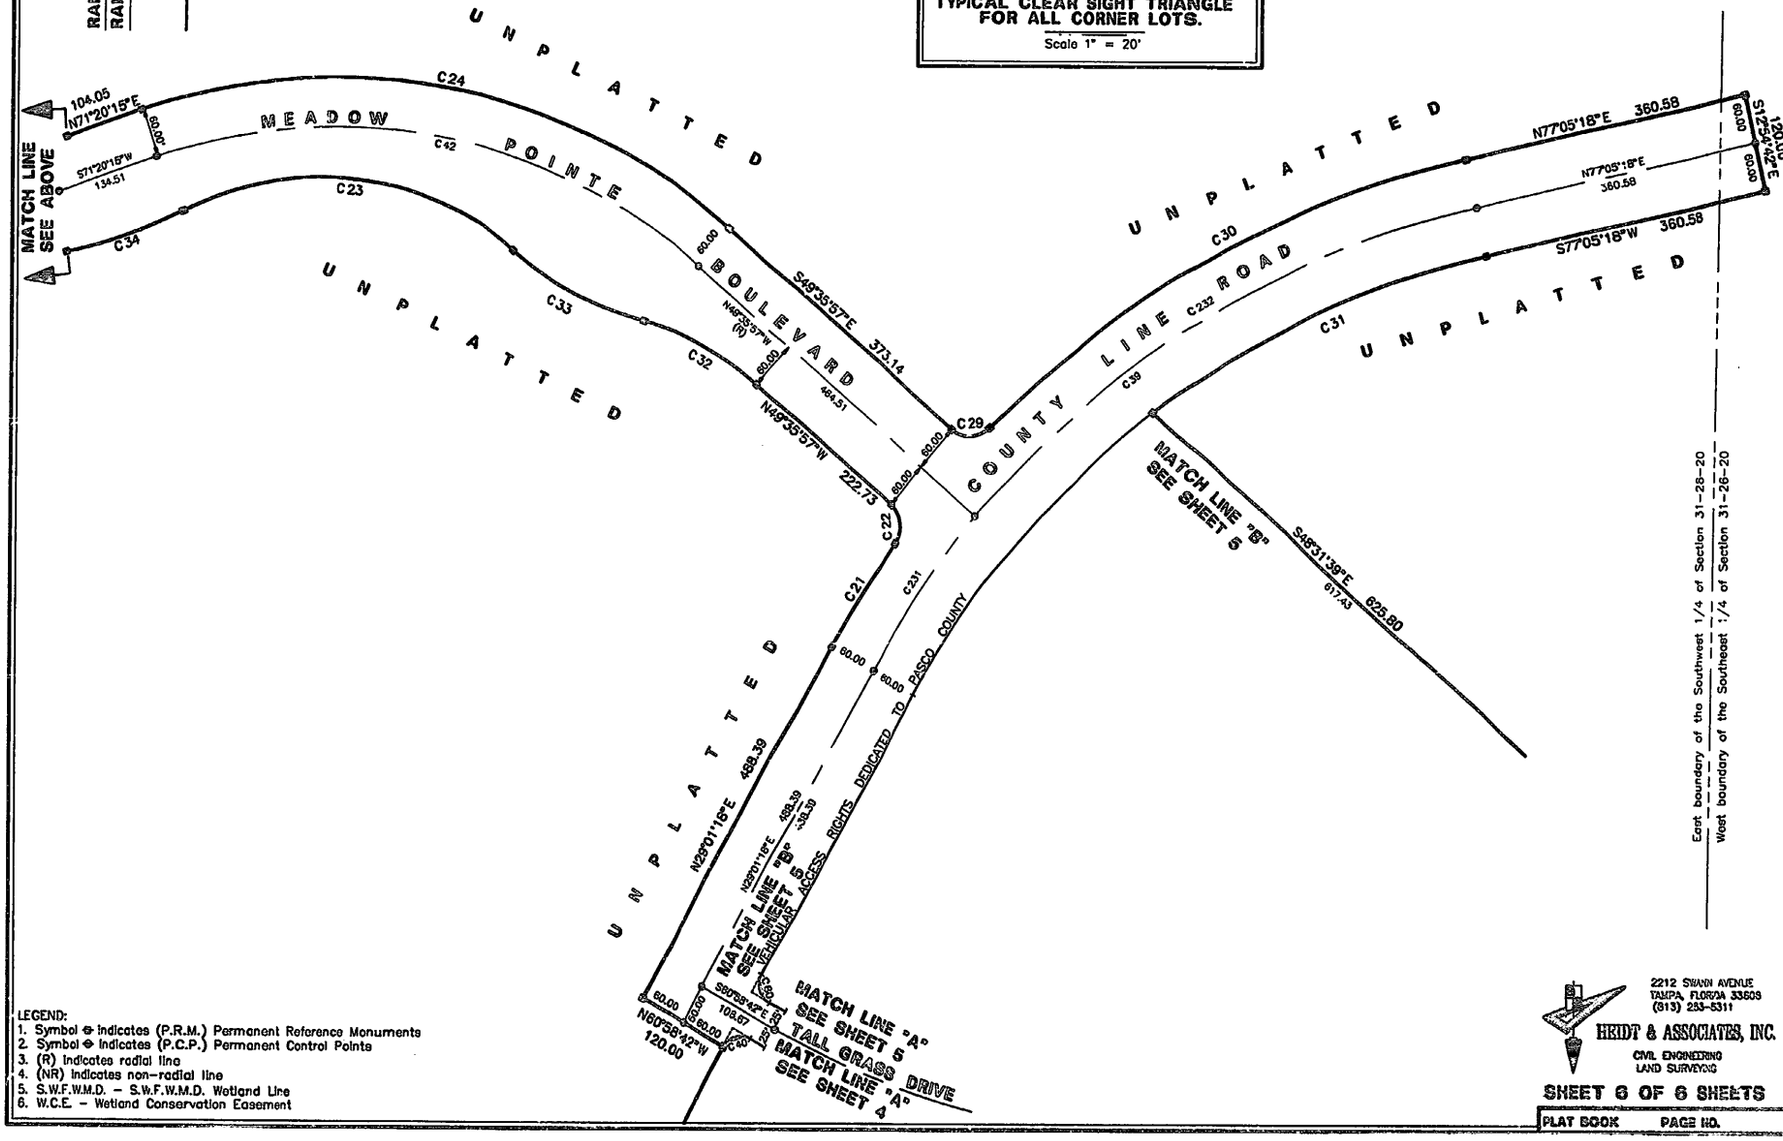

East boundary of the Southwest 1/4 of Section 31-28-20
West boundary of the Southeast 1/4 of Section 31-26-20

LEGEND:
1. Symbol ⊕ indicates (P.R.M.) Permanent Reference Monuments
2. Symbol ⊕ indicates (P.C.P.) Permanent Control Points
3. (R) indicates radial line
4. (NR) indicates non-radial line
5. S.W.F.W.M.D. – S.W.F.W.M.D. Wetland Line
6. W.C.E. – Wetland Conservation Easement

2212 SWANN AVENUE
TAMPA, FLORIDA 33609
(813) 253-5311
HEIDT & ASSOCIATES, INC.
CIVIL ENGINEERING
LAND SURVEYING

SHEET 6 OF 6 SHEETS

PLAT BOOK PAGE NO.